ETAPAS	POTENCIA INSTALADA
ETAPA N°1	57,6 MW
ETAPA N°2	4,8 MW
ETAPA N°3	4,8 MW
TOTAL	67,2 MW

SIMBOLOGÍA

- : RESISTENCIA PUESTA A TIERRA.
- : CONECTOR XLPE 34,5kV
- : CONECTOR SF6 TIPO C / XLPE 34,5kV
- : CONDENSADOR DE ACOPLAMIENTO.
- : INDICADOR CAPACITIVO PRESENCIA DE TENSIÓN.
- : SENSOR DE TENSIÓN
- 52 : INTERRUPTOR DE PODER 220 kV.
- : PARARRAYO CON CONTADOR DE DESCARGAS.
- : DESCONECTADOR HORIZONTAL MOTORIZADO CON PUESTA A TIERRA.
- : DESCONECTADOR HORIZONTAL MOTORIZADO.
- : TRANSFORMADOR DE CORRIENTE TOROIDAL.
- : TRANSFORMADOR DE POTENCIAL.
- : TRANSFORMADOR DE CORRIENTE.

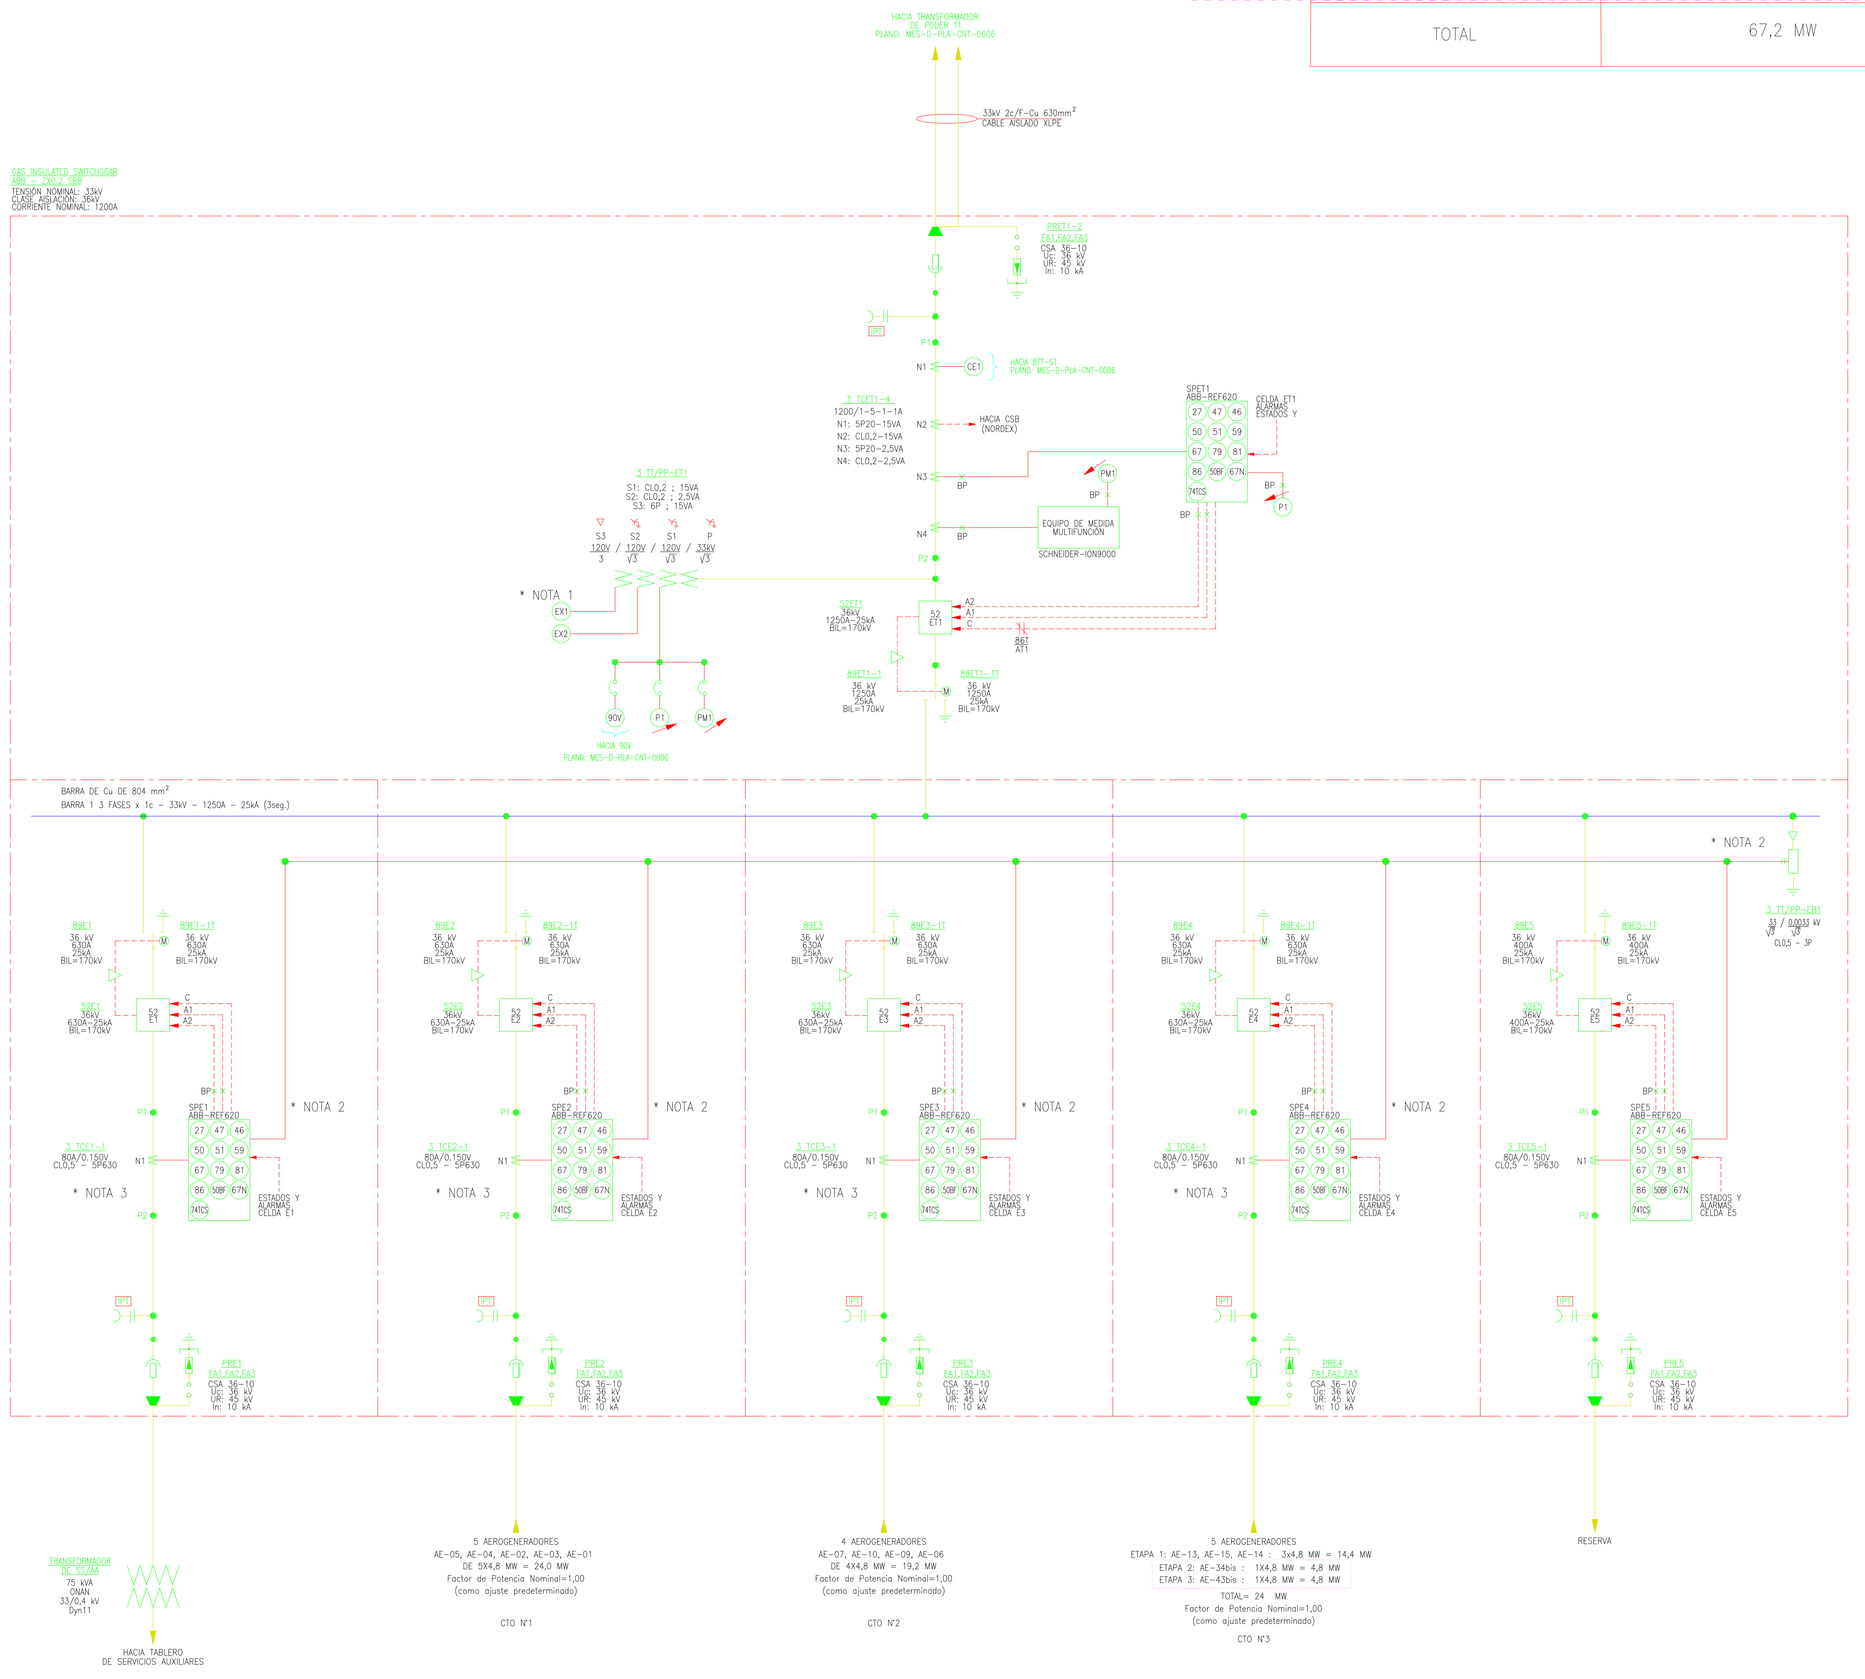

NOMENCLATURA

M	MECANISMO MOTORIZADO
21/21N	PROTECCIÓN DE DISTANCIA
67	PROTECCIÓN DIRECCIONAL
25	VERIFICADOR DE SINCRONISMO
27	PROTECCIÓN BAJO VOLTAJE
59	PROTECCIÓN SOBRE VOLTAJE
50BF	PROTECCIÓN FALLA APERTURA DE INTERRUPTOR
51	PROTECCIÓN SOBRECORRIENTE TEMPORIZADA
50	PROTECCIÓN SOBRECORRIENTE INSTANTANEA
79	RECONEXIÓN
87	PROTECCIÓN DIFERENCIAL
81	PROTECCIÓN DE FRECUENCIA
49T	TEMPERATURA DEVANADOS DEL TRANSFORMADOR
63T	RELÉ BUCHHOLZ DEL TRANSFORMADOR
71T	NIVEL DE ACEITE DEL TRANSFORMADOR
20T	DESCARGA SOBRE PRESIÓN DEL TRANSFOPRMADOR
26T	TEMPERATURA DEL ACEITE
85A	ACELERACIÓN DE ZONA
85C	COMPARACIÓN DIRECCIONAL
85D	TRANSFERENCIA DE DESENGANCHE DIRECTO (TDD)
86	RELÉ MAESTRO
BP	BLOQUE DE PRUEBA
CP	CONTROLADOR DE PAÑO
IT	IMAGEN TÉRMICA
90V	REGULADOR DE TENSIÓN
OSC	OSCILOPERTURBÓGRAFO

NOTAS:

1.- LA TERCERA BOBINA DEL TRANSFORMADOR DE POTENCIAL, CONECTADA EN DELTA HACIA IMPEDANCIA CON EL FIN DE EVITAR FERRORESONANCIA,
2.- EL MEDIDOR DE TENSIÓN SE CONECTA EN LAZO CERRADO DE COMUNICACIÓN VÍA ETHERNET, IEC 61850, HACIA CADA IED.
3.- EQUIPO SENSOR DE CORRIENTE, BASADO EN EL PRINCIPIO DE LA BOBINA DE ROGOWSKI EN SU FUNCIONAMIENTO.

N°	FECHA	MODIFICACIONES	EJEC.	REV.	APR.
05	16.05.22	MODIFICACION ETAPAS DEL PROYECTO	R.S.	Y.S.	V.F.
04	03.02.22	MODIFICACION AEROGENERADORES RED M.T.	R.S.	Y.S.	V.F.
03	08.09.20	EMITIDO PARA CONSTRUCCIÓN	E.S.O.	A.R.H.	C.Y.C.
02	24.08.20	EMITIDO PARA CONSTRUCCIÓN	E.S.O.	A.R.H.	C.Y.C.
01	15.07.20	VALIDO PARA CONSTRUCCIÓN	E.S.O.	A.R.H.	C.Y.O.
00	02.07.20	VALIDO PARA CONSTRUCCIÓN	E.S.O.	A.R.H.	C.Y.O.
0C	01.07.20	EMITIDO PARA APROBACIÓN	E.S.O.	A.R.H.	C.Y.O.
0B	08.06.20	EMITIDO PARA APROBACIÓN	E.S.O.	A.R.H.	C.Y.O.
0A	07.05.20	EMITIDO PARA REVISIÓN Y COMENTARIOS	E.S.O.	A.R.H.	C.Y.O.
A	24.04.20	EMITIDO PARA REVISIÓN INTERNA	E.S.O.	A.R.H.	C.Y.O.

DESSAU ABENGOA CHILE

DIBUJO	DISEÑO	REVISO	APROBO	ESCALA
E.S.O.	E.S.O.	A.R.H.	C.Y.O.	S/N ESCALA

PLANO N° DT3290-10-CP-PLA-006-L02 REV. 02 FECHA JUL.2020

N°	FECHA	REVISIONES	REVISÓ	CONTROLÓ	APROBÓ

AES Gener energía confiable

INSTALACIÓN: SUBESTACIÓN MESAMÁVIDA

ÁREA: S/E MESAMÁVIDA GIS 33kV

DESCRIPCIÓN: DIAGRAMA UNILINEAL FUNCIONAL SUBESTACIÓN MESAMÁVIDA 154/33kV GIS 33kV

PLANO N°: MES-D-PLA-CNT-0007-L2

PROYECTO:	REVISÓ:	APROBÓ:	FECHA INICIAL:
			24-04-20