



Queda totalmente prohibida la reproducción total o parcial de este dibujo sin la autorización expresa y por escrito del propietario.

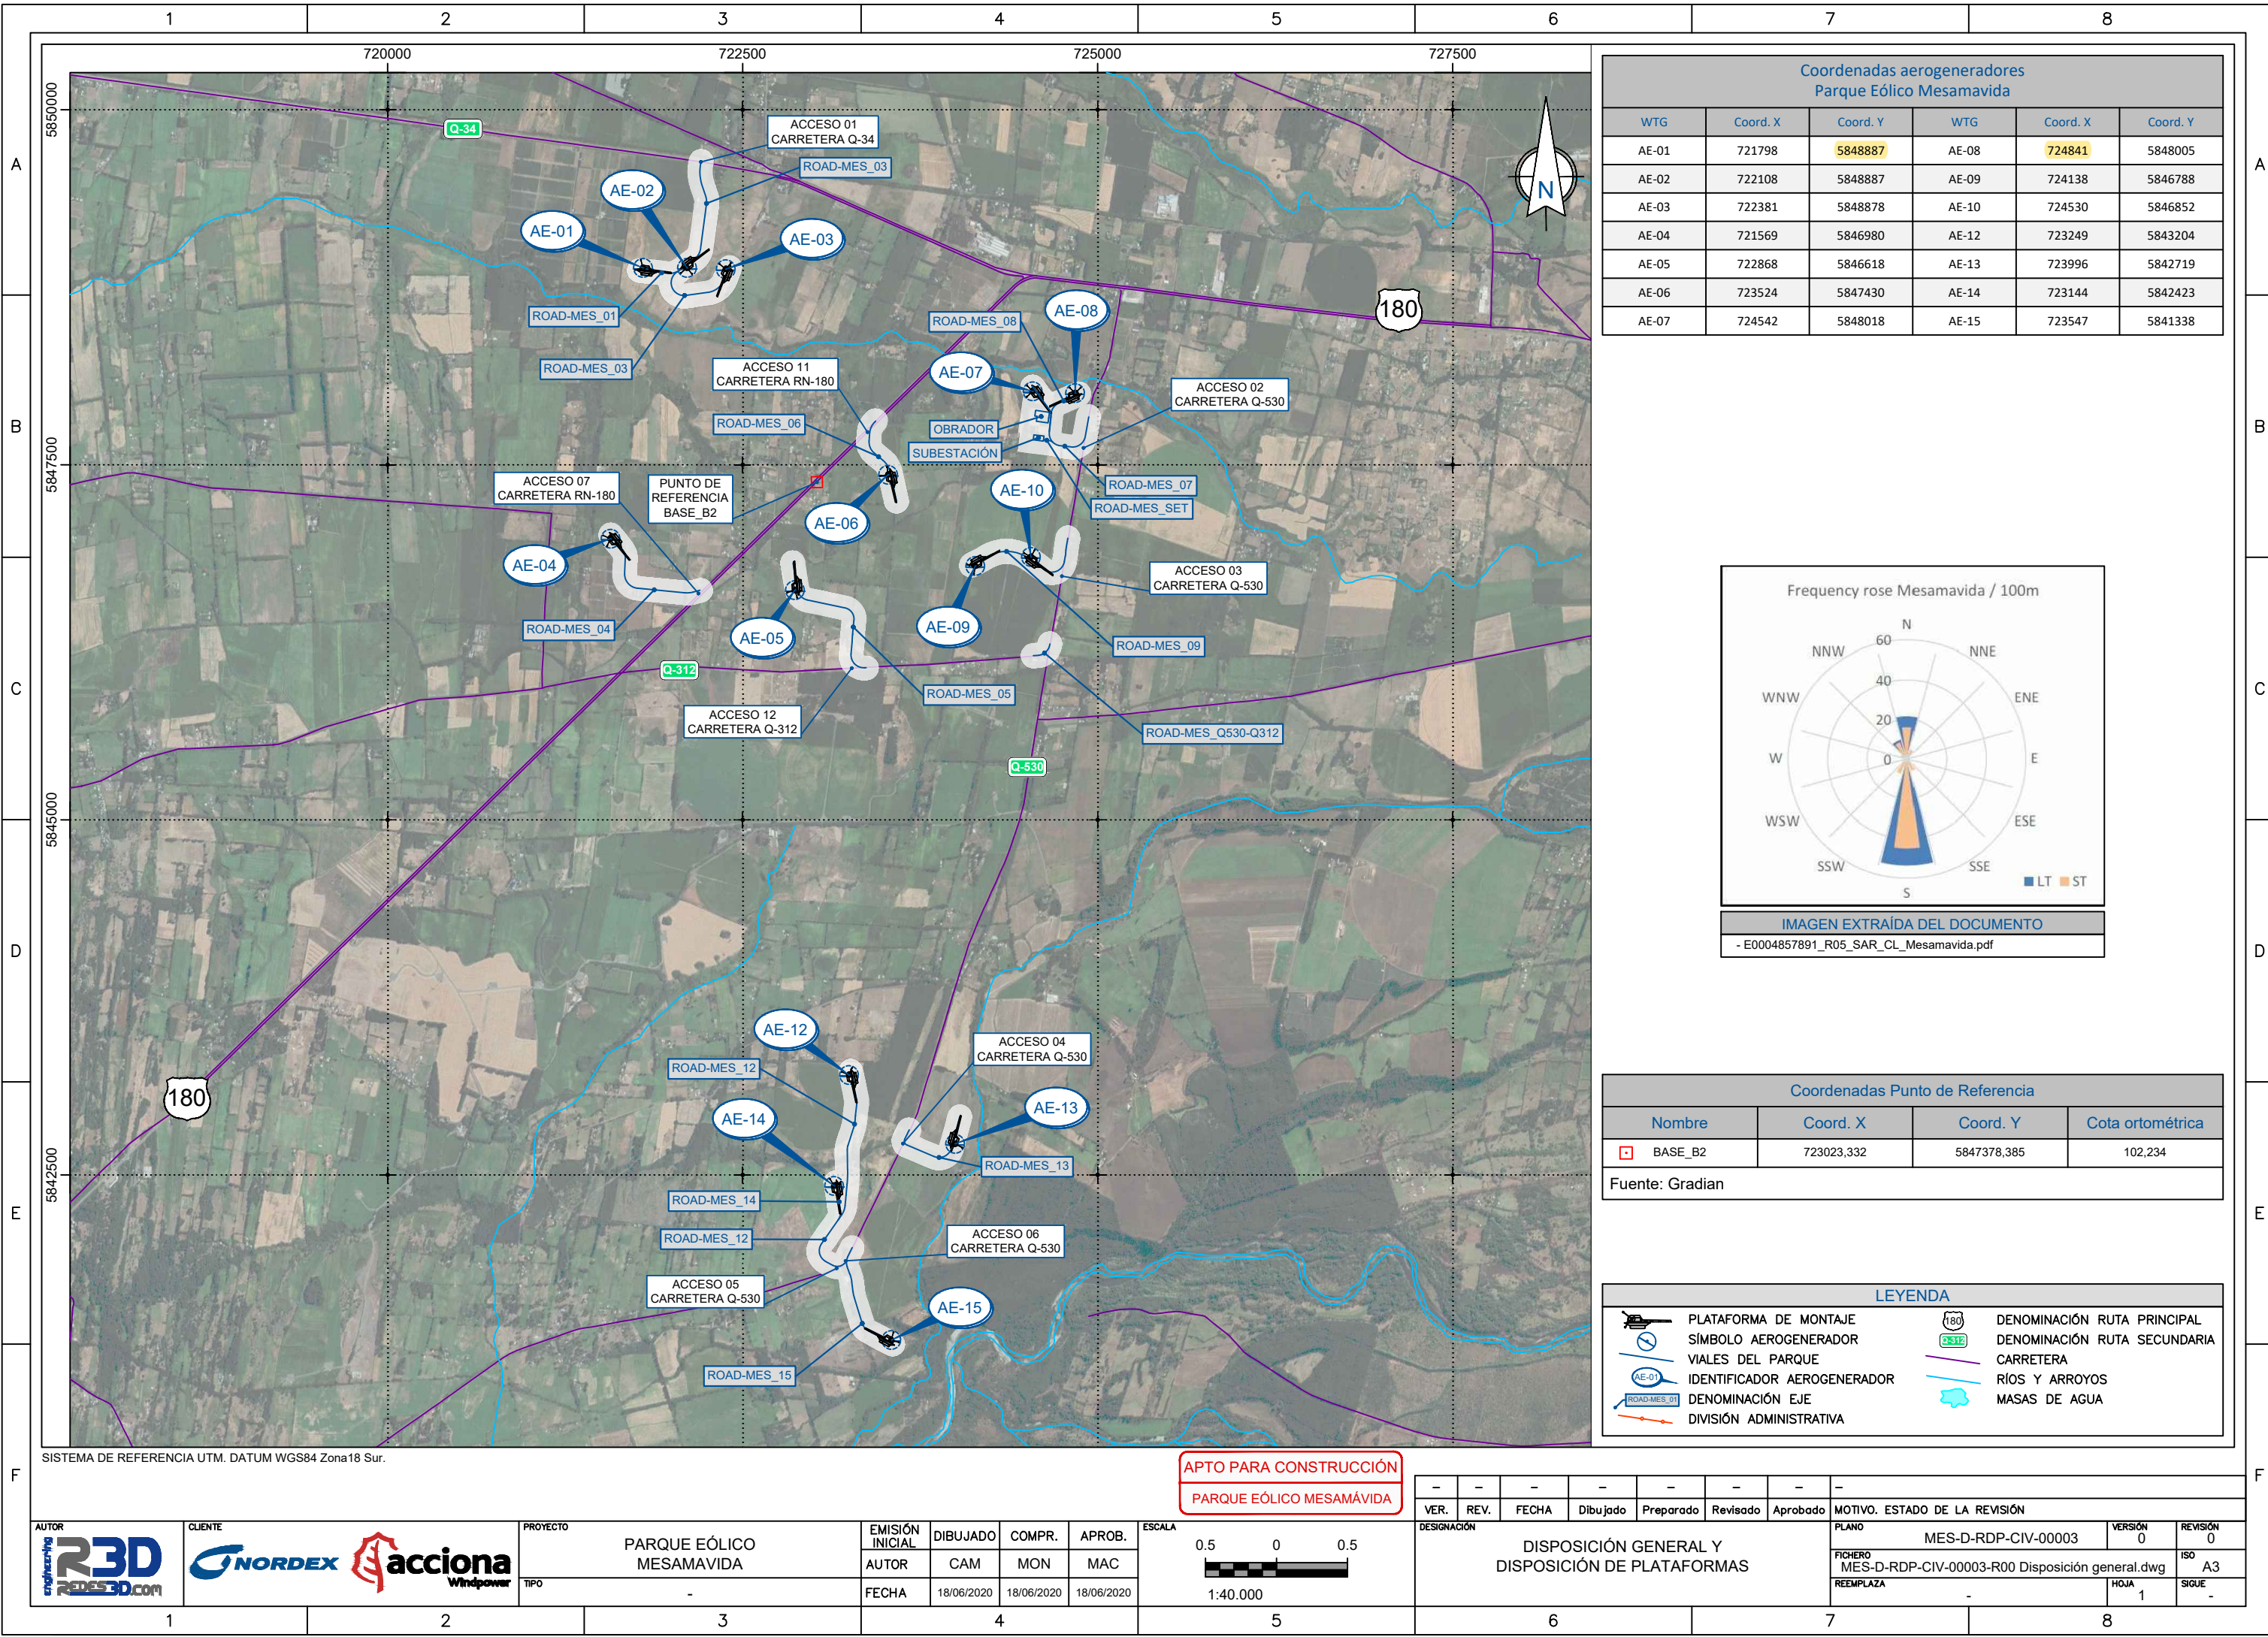

Coordenadas aerogeneradores Parque Eólico Mesamavida					
WTG	Coord. X	Coord. Y	WTG	Coord. X	Coord. Y
AE-01	721798	5848887	AE-08	724841	5848005
AE-02	722108	5848887	AE-09	724138	5846788
AE-03	722381	5848878	AE-10	724530	5846852
AE-04	721569	5846980	AE-12	723249	5843204
AE-05	722868	5846618	AE-13	723996	5842719
AE-06	723524	5847430	AE-14	723144	5842423
AE-07	724542	5848018	AE-15	723547	5841338

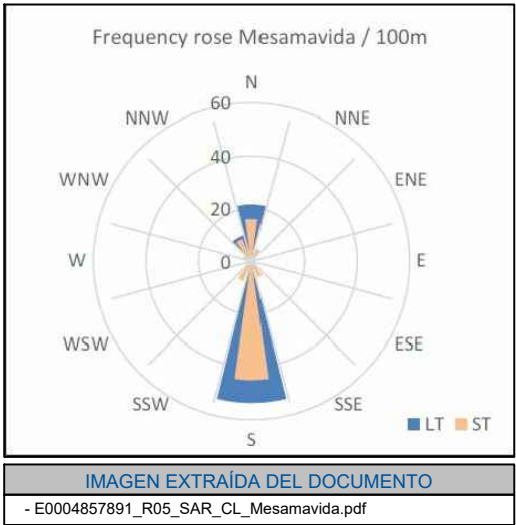

Coordenadas Punto de Referencia			
Nombre	Coord. X	Coord. Y	Cota ortométrica
BASE_B2	723023,332	5847378,385	102,234

Fuente: Gradian

LEYENDA			
	PLATAFORMA DE MONTAJE		DENOMINACIÓN RUTA PRINCIPAL
	SÍMBOLO AEROGENERADOR		DENOMINACIÓN RUTA SECUNDARIA
	VIALES DEL PARQUE		CARRETERA
	IDENTIFICADOR AEROGENERADOR		RÍOS Y ARROYOS
	DENOMINACIÓN EJE		MASAS DE AGUA
	DIVISIÓN ADMINISTRATIVA		

SISTEMA DE REFERENCIA UTM. DATUM WGS84 Zona18 Sur.

APTO PARA CONSTRUCCIÓN
PARQUE EÓLICO MESAMÁVIDA



PROYECTO
PARQUE EÓLICO
MESAMÁVIDA

EMISIÓN INICIAL
AUTOR
CAM
MON
MAC
FECHA
18/06/2020
18/06/2020
18/06/2020

ESCALA
0.5 0 0.5
1:40.000

VER.	REV.	FECHA	Dibujado	Preparado	Revisado	Aprobado	MOTIVO. ESTADO DE LA REVISIÓN
-	-	-	-	-	-	-	PLANO MES-D-RDP-CIV-00003 VERSIÓN 0 REVISIÓN 0
DESIGNACIÓN DISPOSICIÓN GENERAL Y DISPOSICIÓN DE PLATAFORMAS							FICHERO MES-D-RDP-CIV-00003-R00 Disposición general.dwg ISO A3
							REEMPLAZA - HOJA 1 SIGUE -