





P.E. SAN MATÍAS. CIRCUITO 1

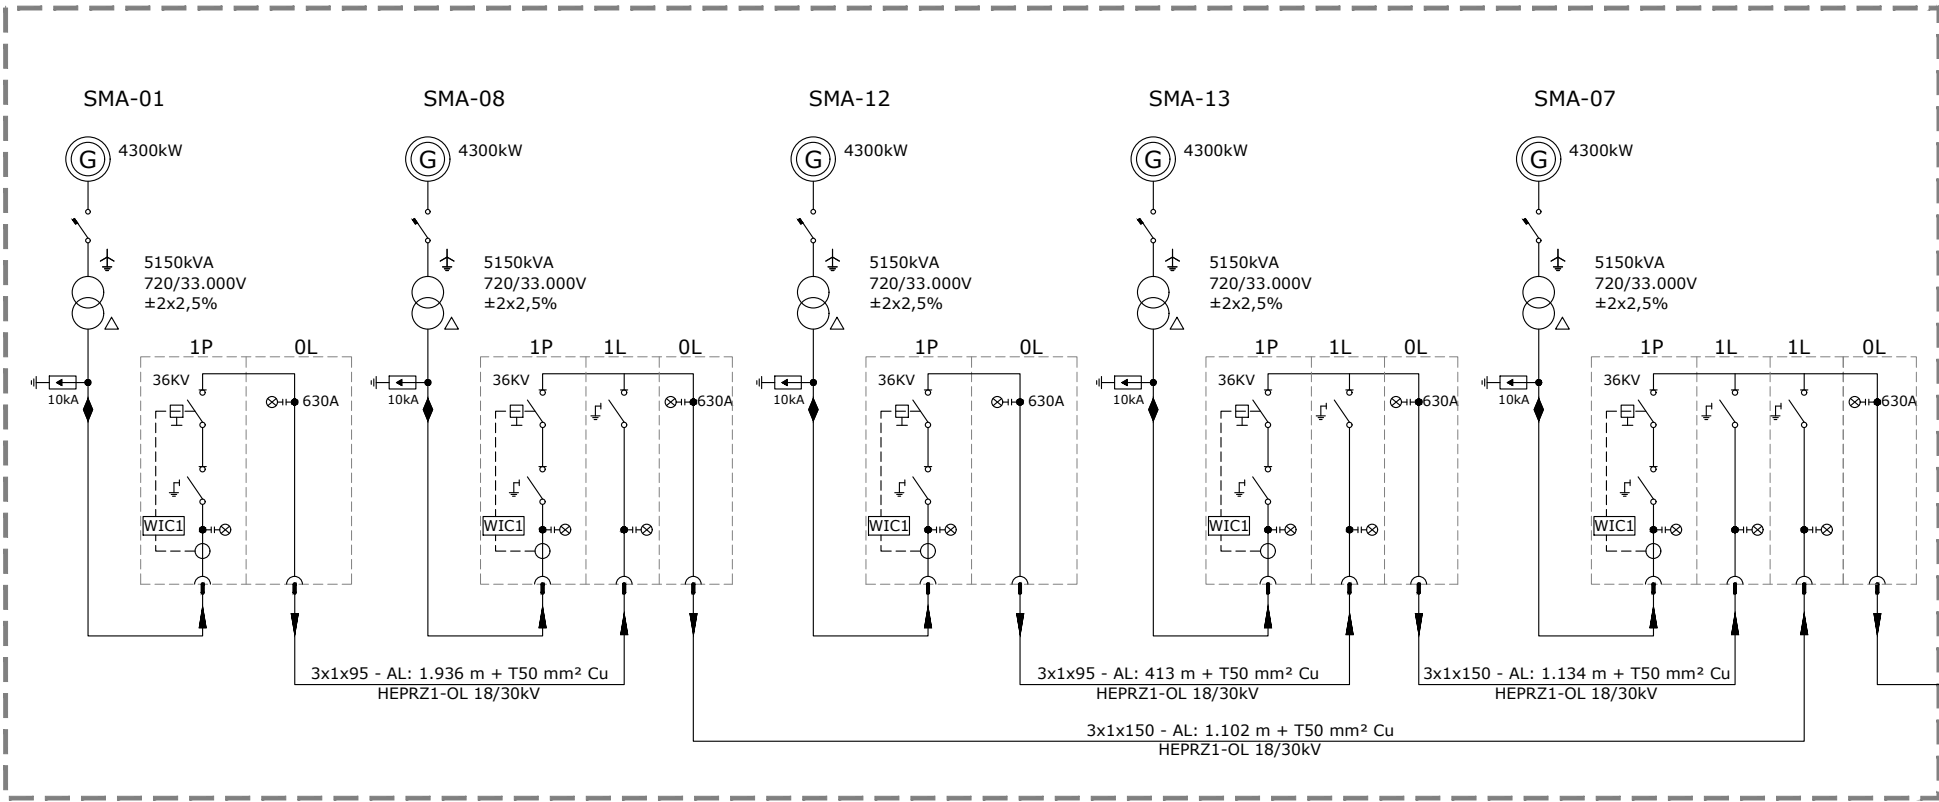

SUBESTACIÓN P.E. CAMPO LINDO (33/220kV)

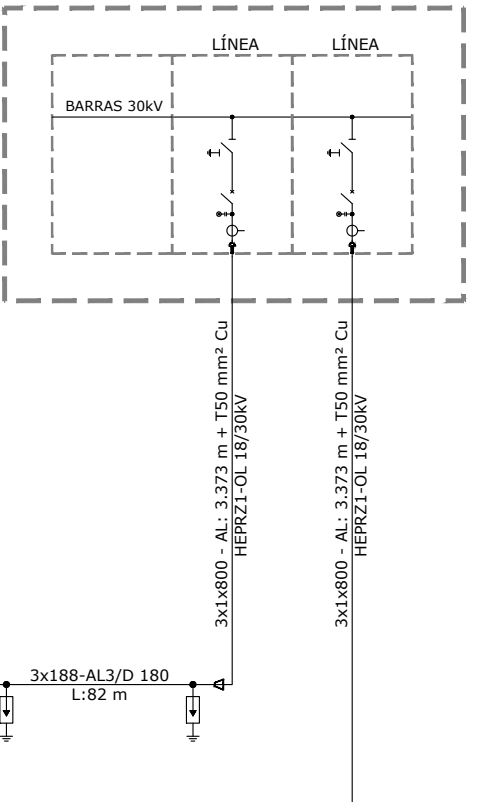

P.E. SAN MATÍAS. CIRCUITO 2

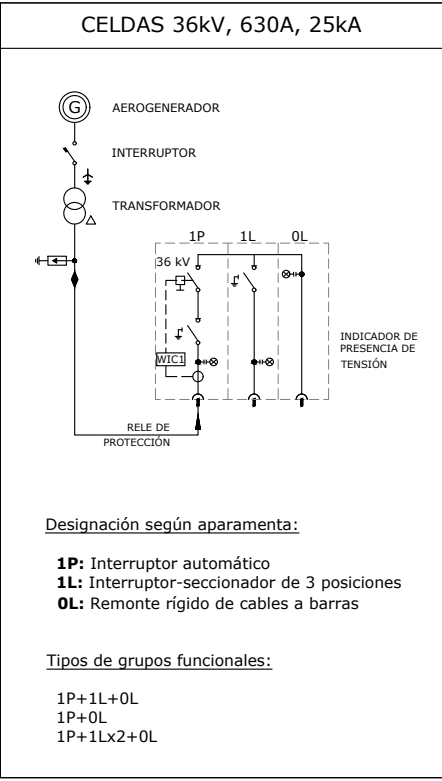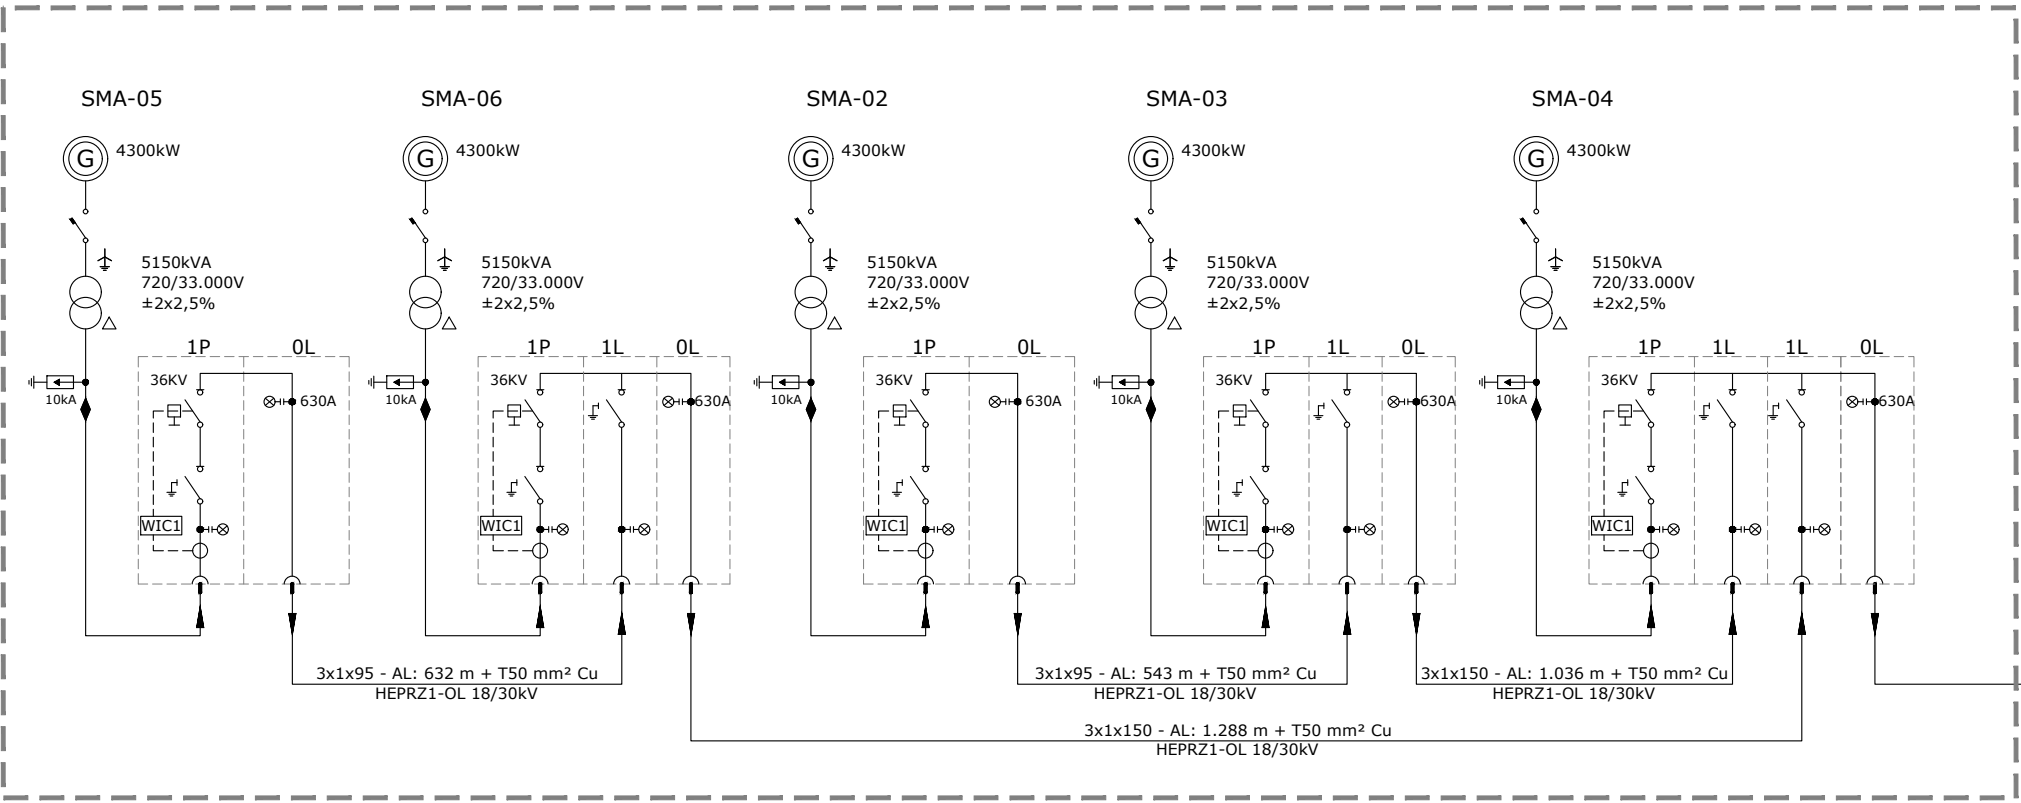

Designación según aparamenta:

- 1P: Interruptor automático
- 1L: Interruptor-seccionador de 3 posiciones
- OL: Remonte rígido de cables a barras

Tipos de grupos funcionales:

- 1P+1L+OL
- 1P+OL
- 1P+1Lx2+OL

DOCUMENTOS DE REFERENCIA

- OE-3-CAL-6-MC-01_Memoria de cálculo - Red de media tensión
- OE-3-CAL-6-DW-04_RMT. Planta general y detalle

Rev.	Fecha	Proyect.	Dibujado	Comprob.	Aprobado	Modificación
OD	20/03/23	A.O.L.	A.C.F.	G.D.S.	A.B.A.	SEGUNDA REVISIÓN
OC	14/02/23	A.O.L.	A.C.F.	G.D.S.	A.B.A.	PRIMERA REVISIÓN
OB	30/09/22	A.O.L.	A.C.F.	G.D.S.	A.B.A.	EMISIÓN INICIAL
Rev.	Fecha	Proyect.	Dibujado	Comprob.	Aprobado	Modificación

PARQUE EÓLICO SAN MATÍAS (CHILE)

RED DE MEDIA TENSIÓN
ESQUEMA UNIFILAR

ms

GES

GLOBAL ENERGY SERVICES

enertech

N° CAD: OE-3-SMA-6-DW-03


REV. OD

HOJA: 01


SIGUE: 02

SISTEMA COORDENADAS UTM WGS84 HUSO 18 S
A3 DIMENSIONES: METROS (m)
ESCALA: S/E




P.E. SAN MATÍAS. CIRCUITO 3

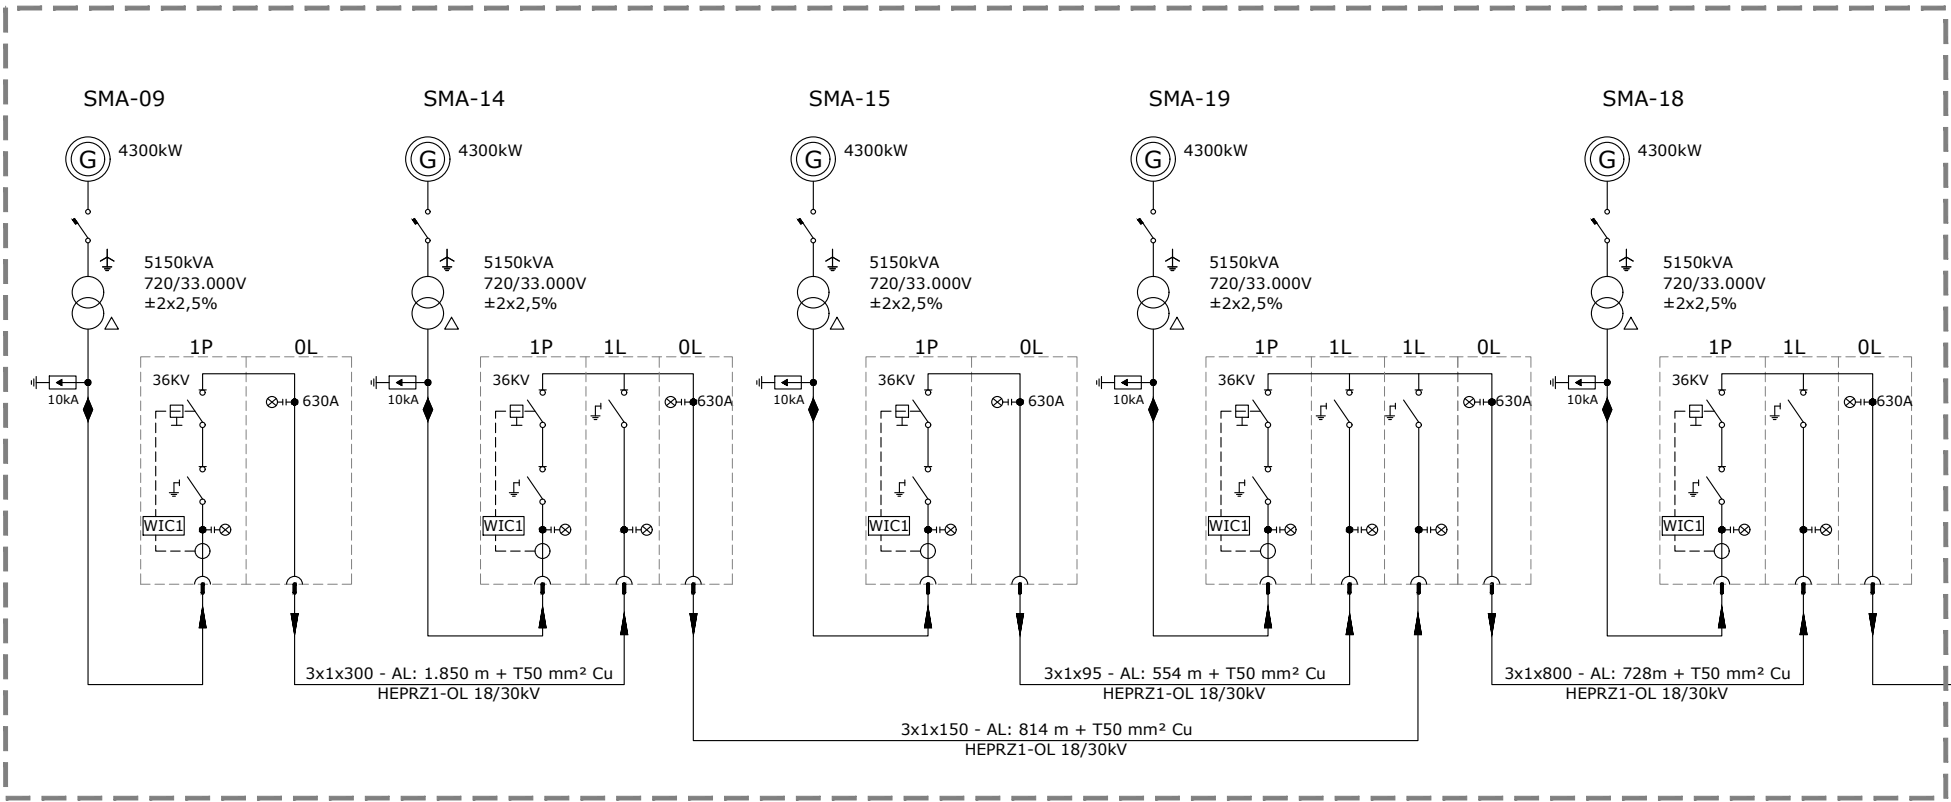

SUBESTACIÓN P.E. CAMPO LINDO (33/220kV)

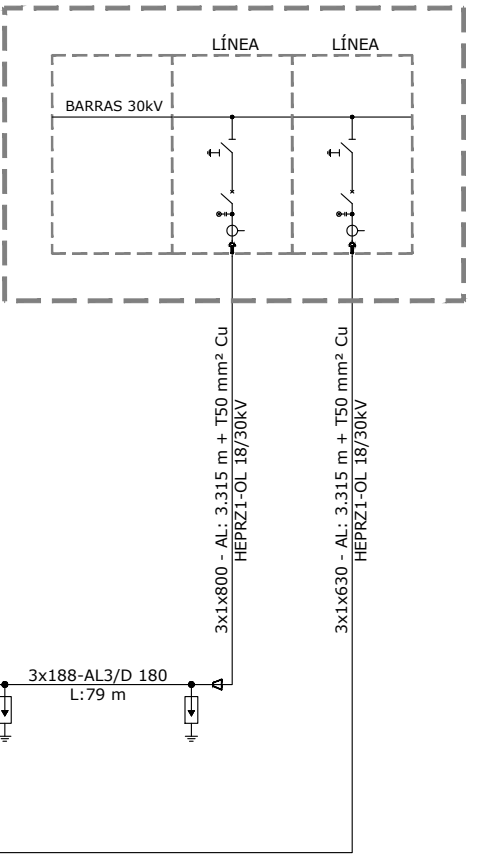

P.E. SAN MATÍAS. CIRCUITO 4

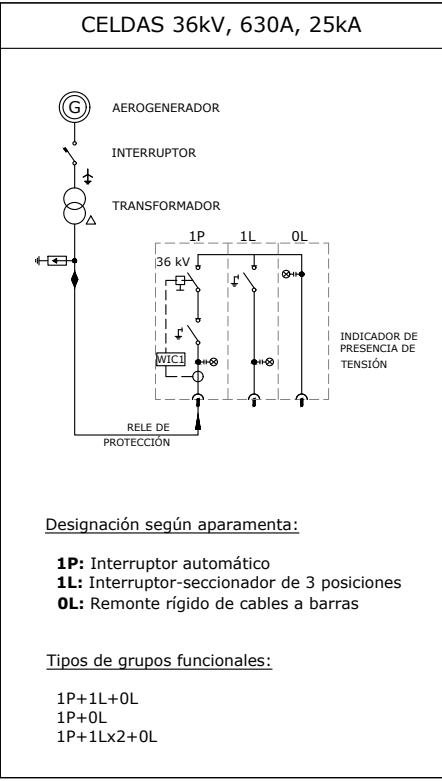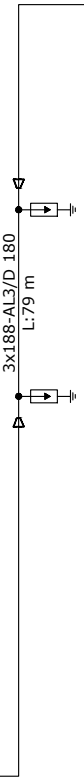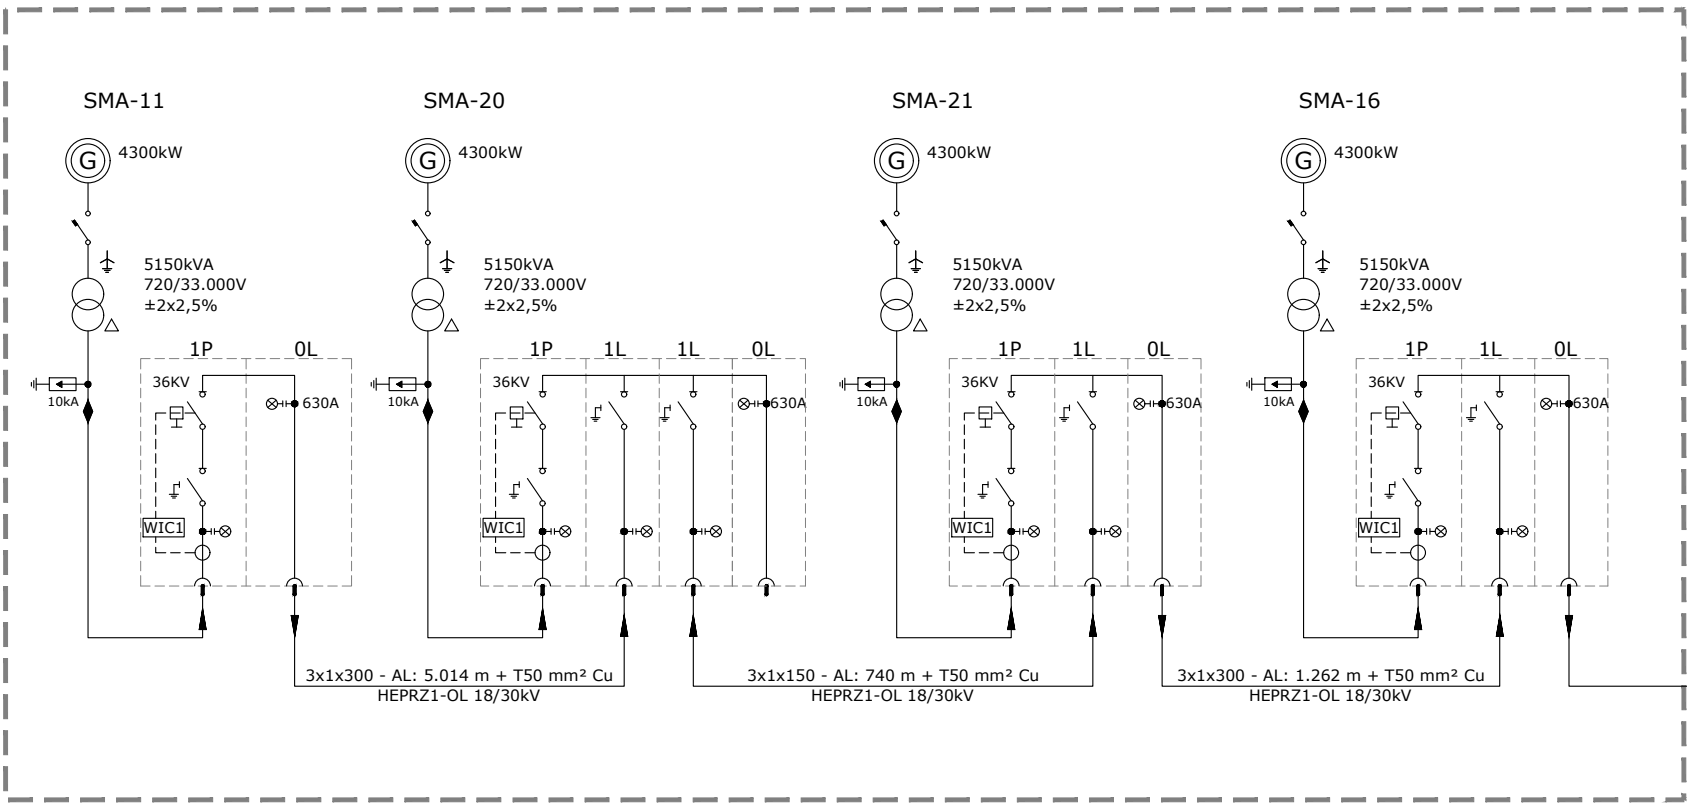

Designación según aparamenta:

- 1P: Interruptor automático
- 1L: Interruptor-seccionador de 3 posiciones
- OL: Remonte rígido de cables a barras

Tipos de grupos funcionales:

- 1P+1L+OL
- 1P+OL
- 1P+1Lx2+OL

DOCUMENTOS DE REFERENCIA

- OE-3-CAL-6-MC-01_Memoria de cálculo - Red de media tensión
- OE-3-CAL-6-DW-04_RMT. Planta general y detalle

Rev.	Fecha	Proyect.	Dibujado	Comprob.	Aprobado	Modificación
OD	20/03/23	A.O.L.	A.C.F.	G.D.S.	A.B.A.	SEGUNDA REVISIÓN
OC	14/02/23	A.O.L.	A.C.F.	G.D.S.	A.B.A.	PRIMERA REVISIÓN
OB	30/09/22	A.O.L.	A.C.F.	G.D.S.	A.B.A.	EMISIÓN INICIAL

SISTEMA COORDENADAS UTM WGS84 HUSO 18 S	A3	DIMENSIONES: METROS (m)
ESCALA:	S/E	

PARQUE EÓLICO SAN MATÍAS (CHILE)

RED DE MEDIA TENSIÓN
ESQUEMA UNIFILAR



N° CAD: 0E-3-SMA-6-DW-03

REV. OD

HOJA: 02

SIGUE: /