


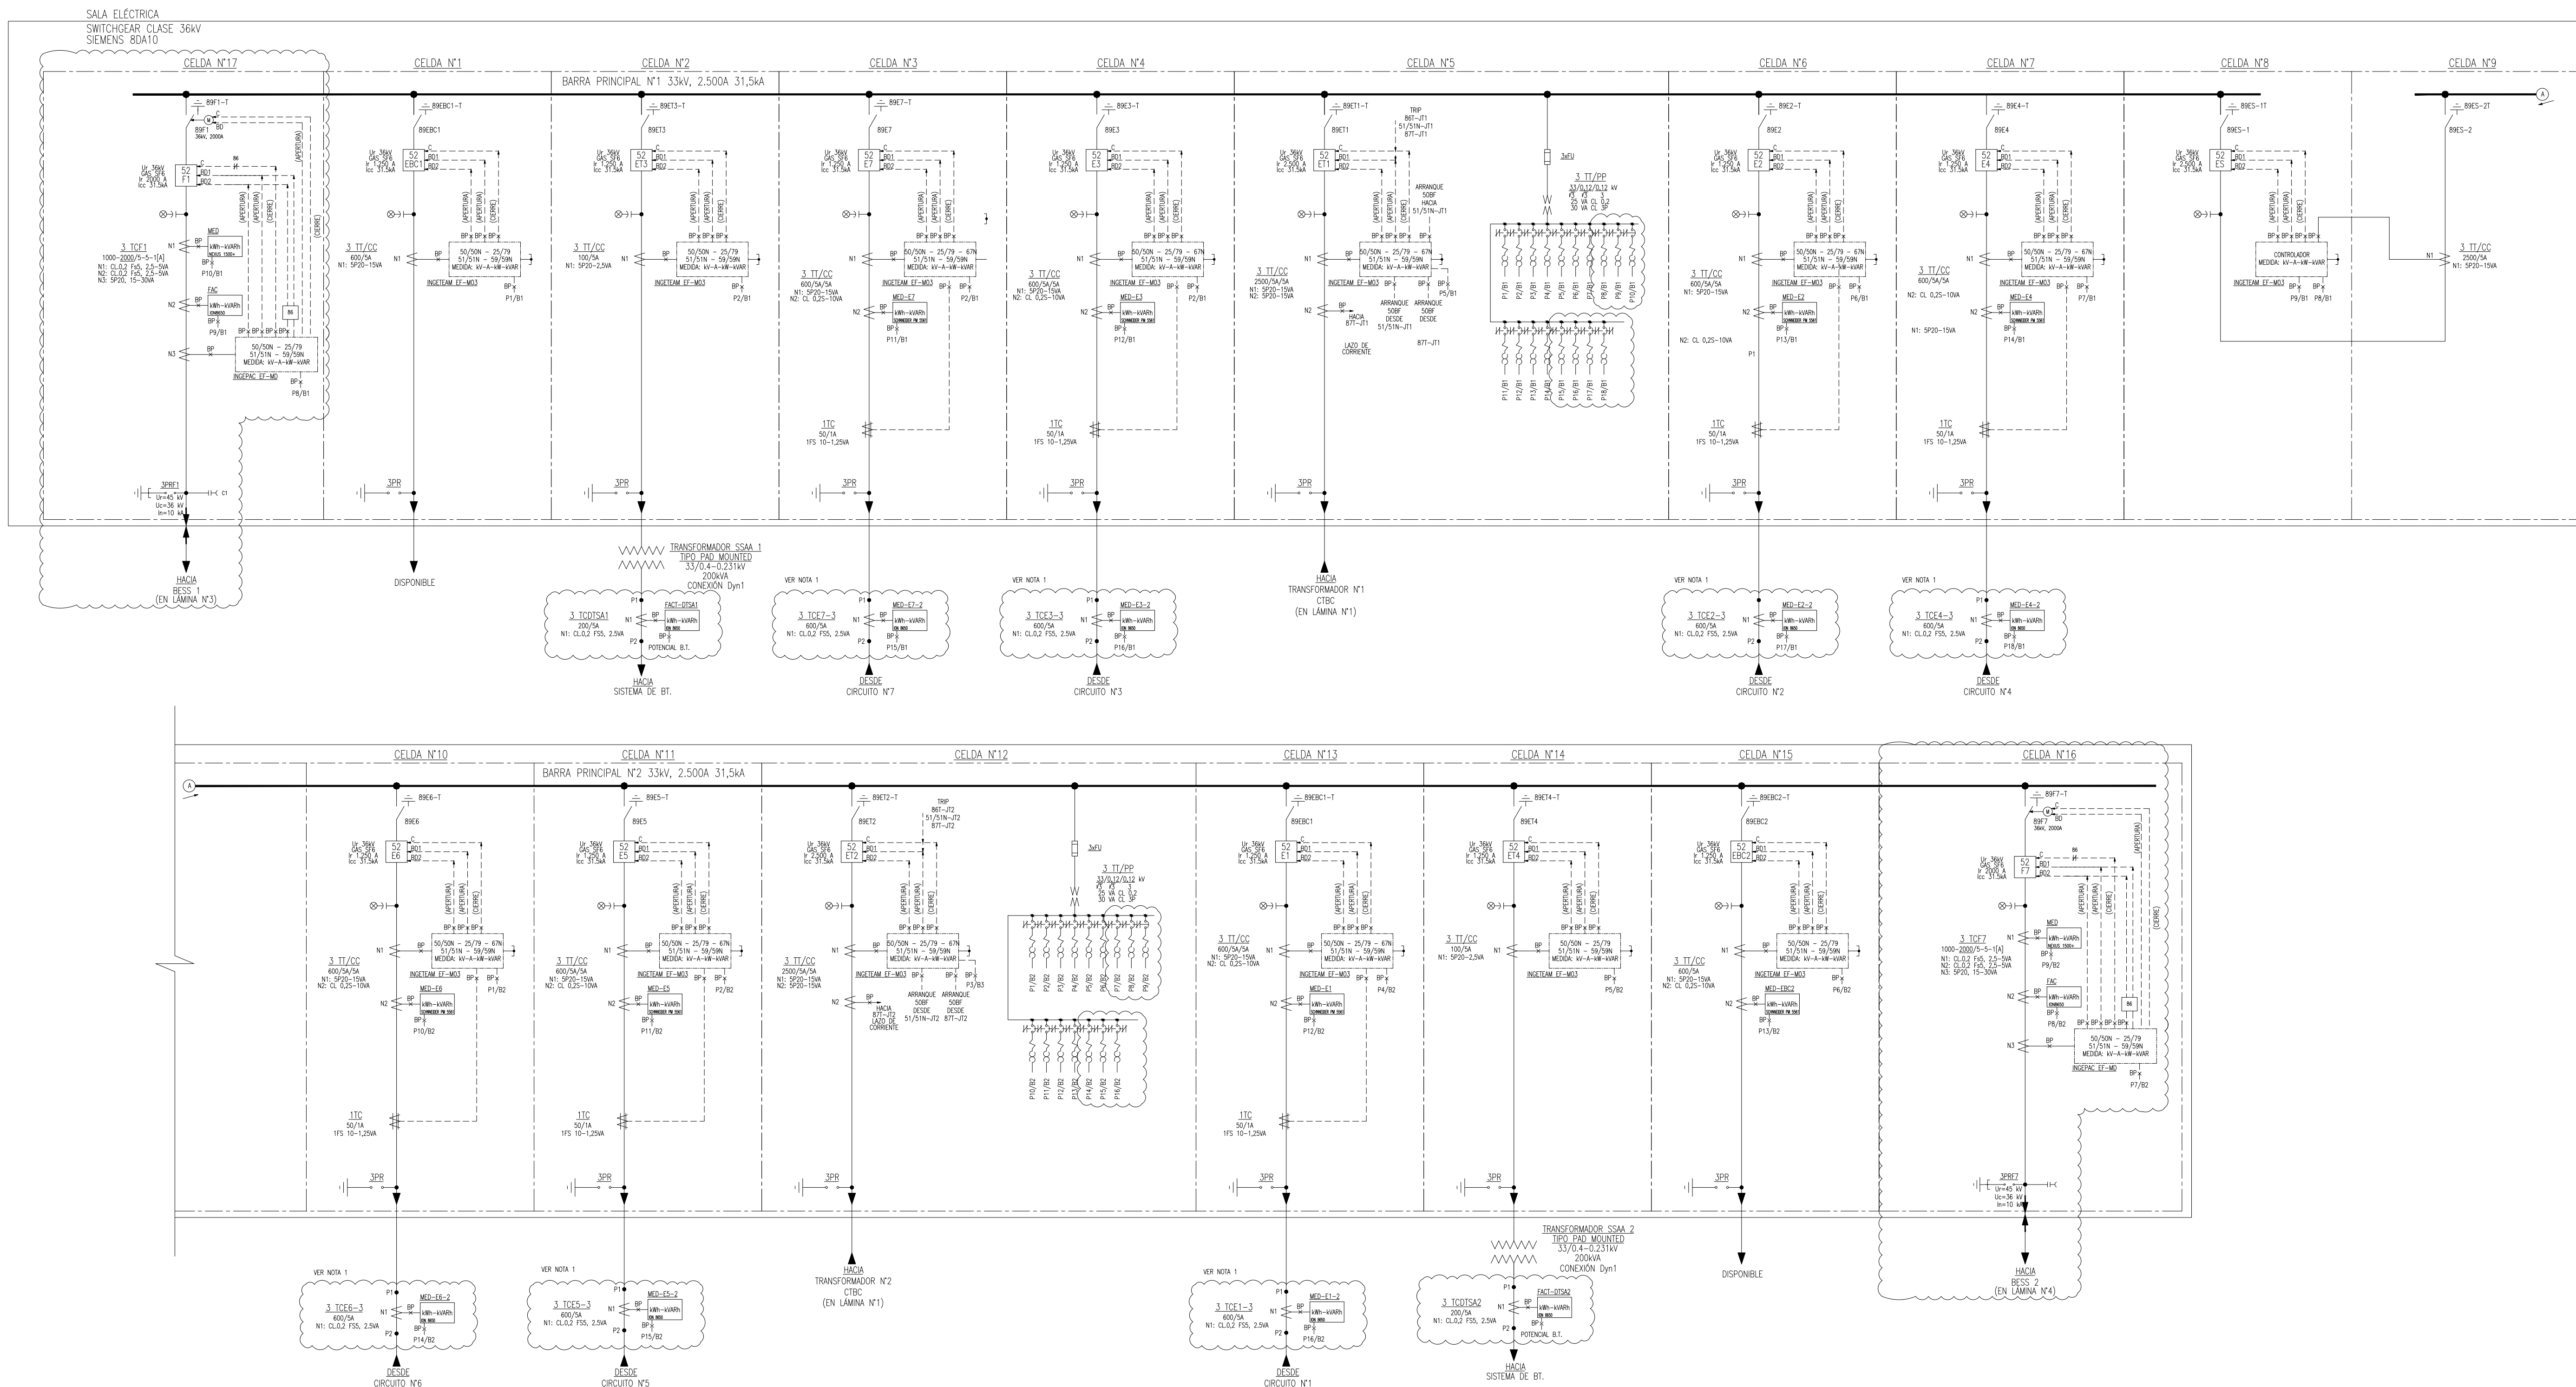

SIMBOLOGÍA:
PROYECTADO



INGENIERÍA DE DETALLES PROYECTO BESS BOLERO




PLANO N°			
23096-01-EE-DU-003			
TÍTULO:			
DIAGRAMA UNILINEAL FUNCIONAL S/E BOLERO 33 kV			
NORMA	REVISIÓN	ESCALA	LÁMINA
	9	INDICADA	2 DE 4

NOTAS:
1. El proyecto considera la instalación de un TC adicional y de un medidor de clase 0,2 adicional para cumplir requerimientos comerciales con nuestro cliente.





REFERENCIA	PLANO/DOCUMENTO N°	DESCRIPCIÓN	REVISIONES	N°	FECHA	DESCRIPCIÓN
			9	24.03.2025	ACTUALIZACIÓN	CEN
			8	18.03.2025	ACTUALIZACIÓN	CEN
			7	12.03.2025	ACTUALIZACIÓN	CEN
			6	11.02.2025	ACTUALIZACIÓN	CEN
			5	08.01.2025	ACTUALIZACIÓN	CEN
			4	27.12.2024	ACTUALIZACIÓN	CEN
			3	24.10.2024	ACTUALIZACIÓN	CEN
			2	12.04.2024	EMITIDO PARA USO	M.C.G. J.Z.V. C.M.P. C.T.C.
			1	15.01.2024	EMITIDO PARA USO	M.C.G. J.Z.V. C.M.P. C.T.C.

DIBUJO	NOMBRE	FECHA
PROYECTÓ	I-SEP	24.10.2024
REVISÓ	I-SEP	24.10.2024
APROBÓ	I-SEP	24.10.2024


AP-87B3

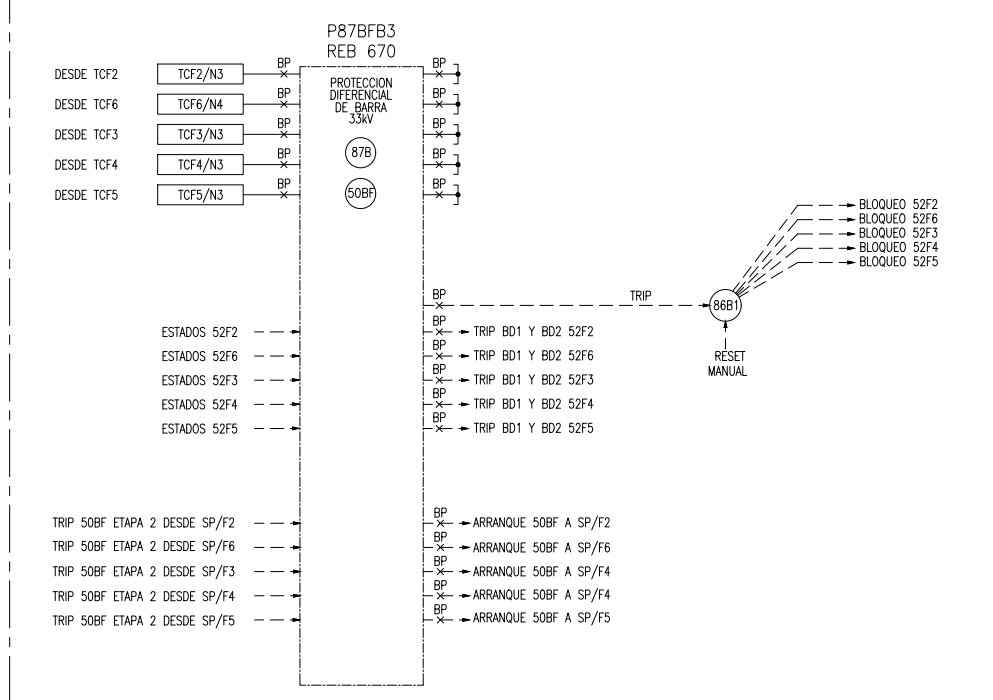

DESDE CELDA N°17
PAÑO F1
EN S/E BOLERO
DESDE LÁMINA N°2
2x3x6,30 mm². CU

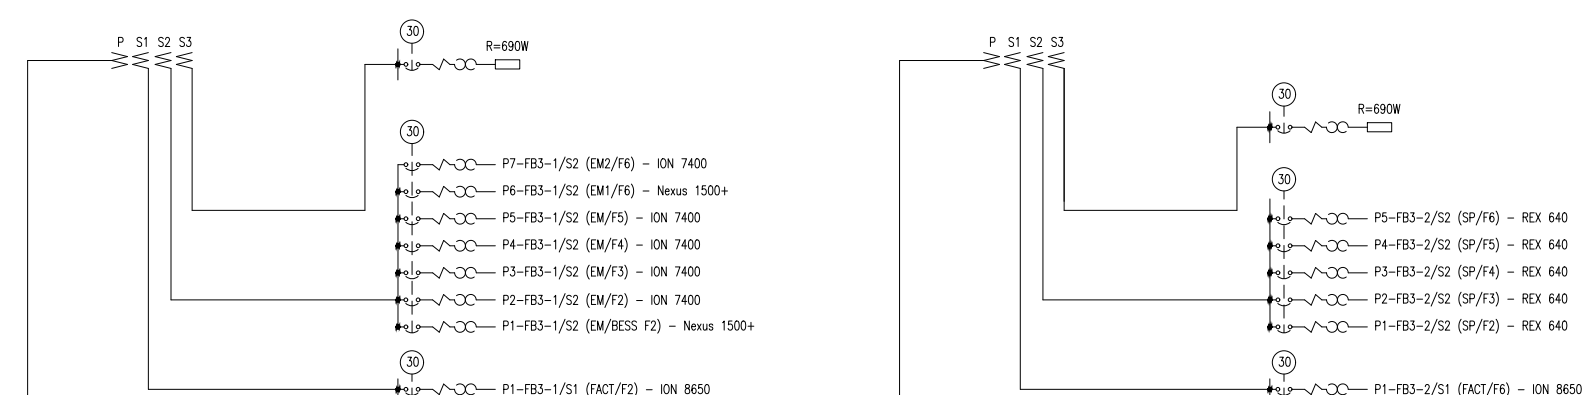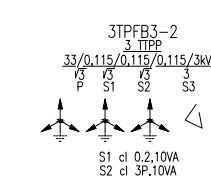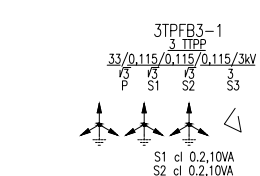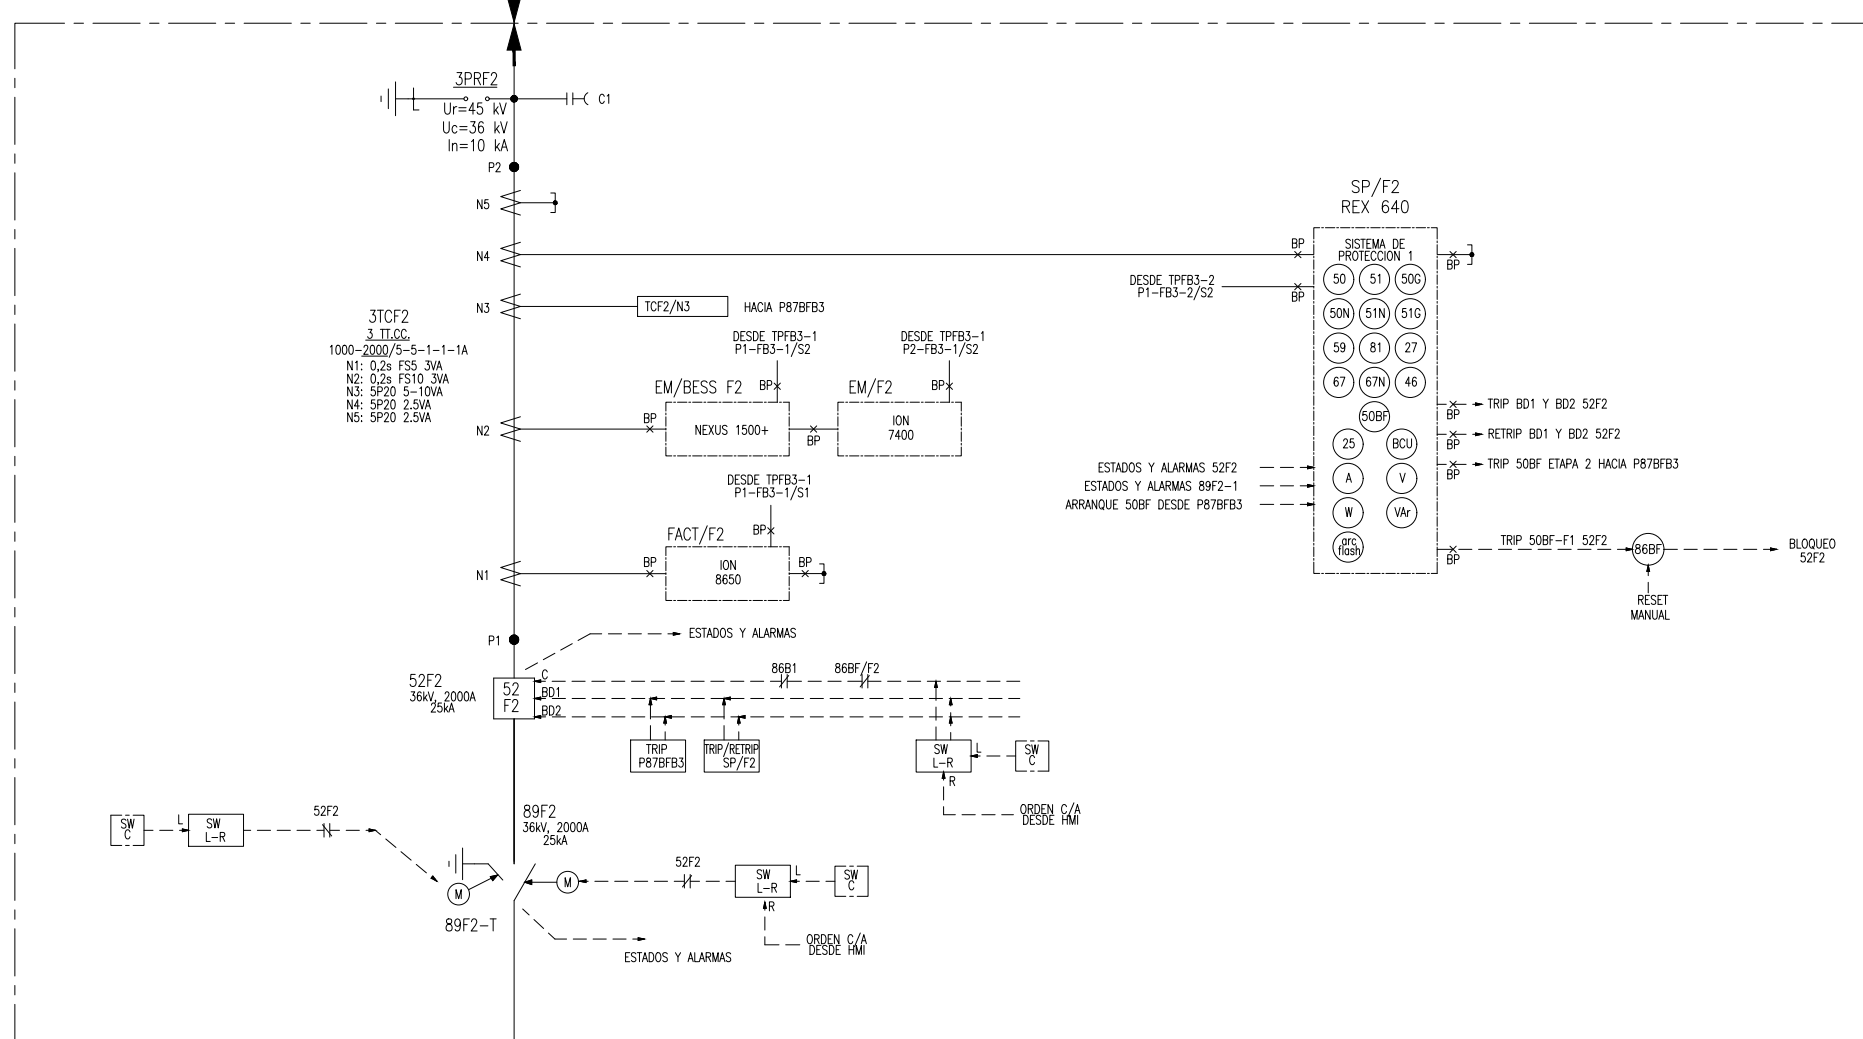

SWITCHGEAR N°1

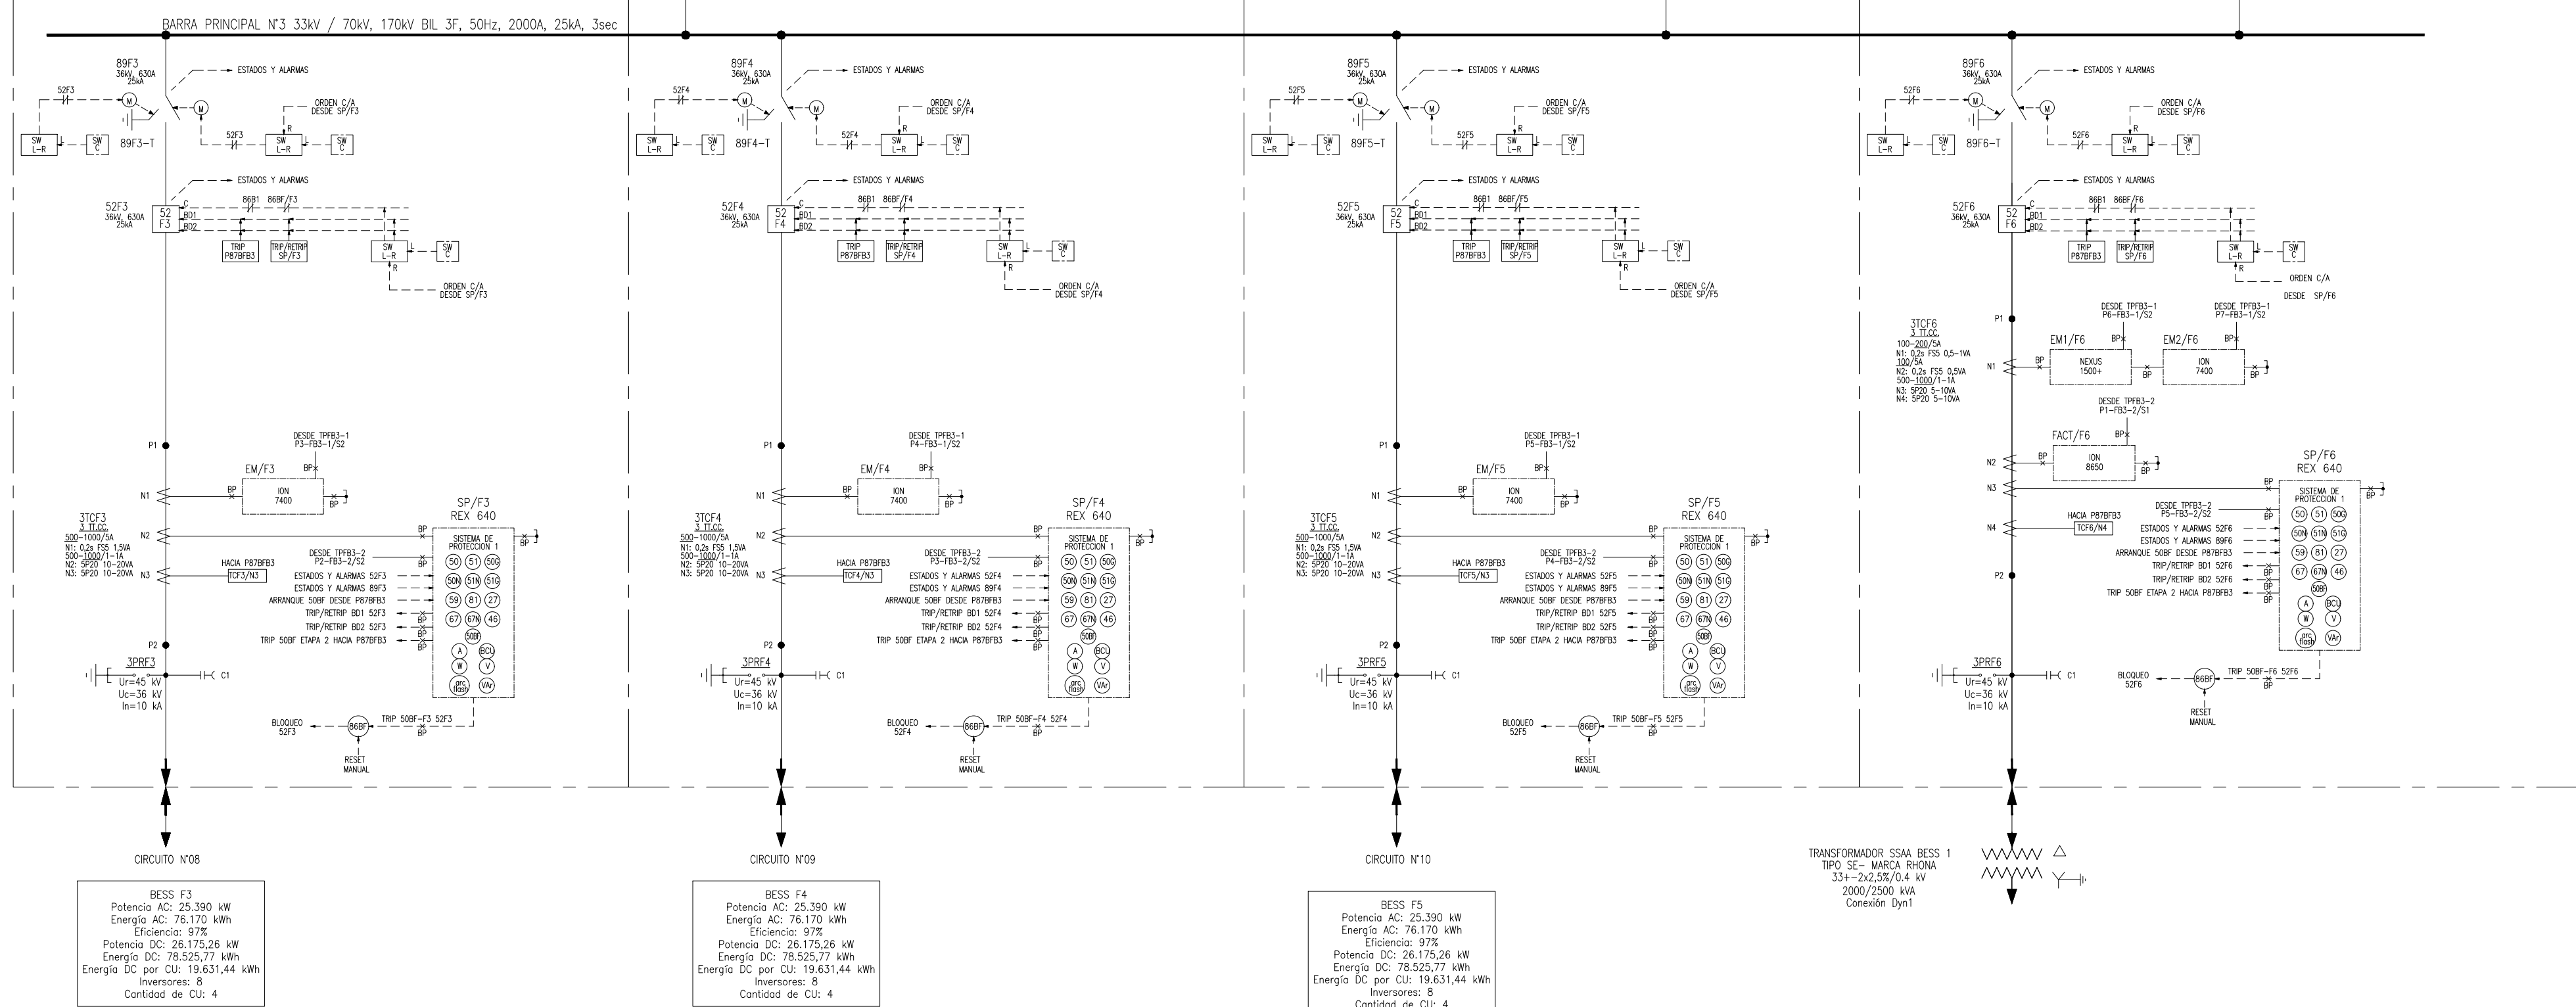

TRANSFORMADOR SSAA BESS 1
TIPO SE- MARCA RHONA
33±2x2,5%/0.4 kV
2000/2500 kVA
Conexión Dyn1



INGENIERÍA DE DETALLES PROYECTO BESS BOLERO

PLANO N°	23096-01-EE-DU-003
----------	--------------------

TÍTULO:

DIAGRAMA UNILINEAL
FUNCIONAL
BESS BOLERO 33kV
SWG 1

NORMA	REVISIÓN	ESCALA	LÁMINA 3 DE 4
	9	INDICADA	



	NOMBRE	FECHA
DIBUJÓ	I-SEP	24.10.2024
PROYECTÓ	I-SEP	24.10.2024
REVISÓ	I-SEP	24.10.2024
APROBÓ	I-SEP	24.10.2024

REFERENCIA	PLANO/DOCUMENTO N°	DESCRIPCIÓN	REVISIONES	REVISIONES			
				N°	FECHA	DESCRIPCIÓN	
				9	24.03.2025	ACTUALIZACIÓN CEN	
				8	18.03.2025	ACTUALIZACIÓN CEN	
				7	12.03.2025	ACTUALIZACIÓN CEN	
				6	11.02.2025	ACTUALIZACIÓN CEN	
				5	18.01.2025	ACTUALIZACIÓN CEN	
				4	27.12.2024	ACTUALIZACIÓN CEN	
				3	24.10.2024	ACTUALIZACIÓN CEN	
				2	12.04.2024	EMITIDO PARA USO	
				1	18.01.2024	EMITIDO PARA USO	
							M.C.G. J.Z.V. C.M.P. C.T.C.
							DELEDO 2020/2021 REVISY APROB

REFERENCIA		
PLANO/DOCUMENTO N°		DESCRIPCIÓN

[illegible]

DESDE CELDA N°16
PAÑO F7
EN S/E BOLERO
DESDE LÁMINA N°2
2x3x630 mm², CU

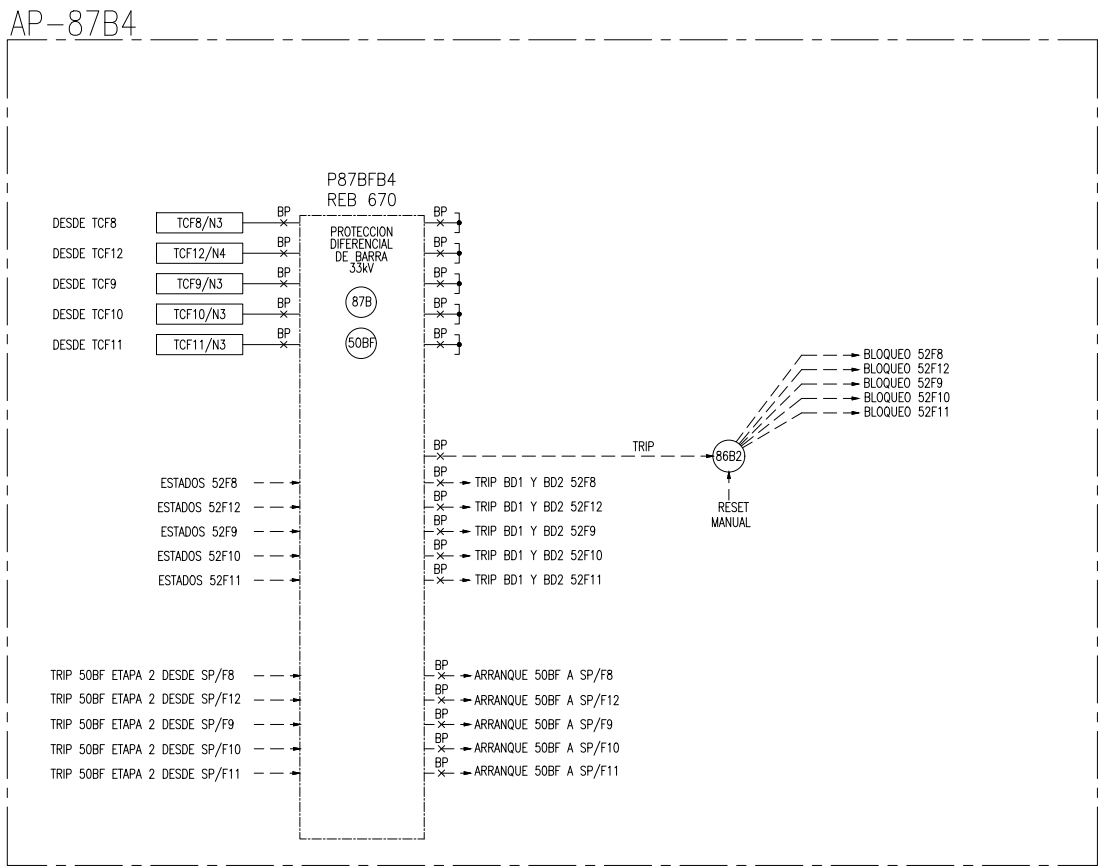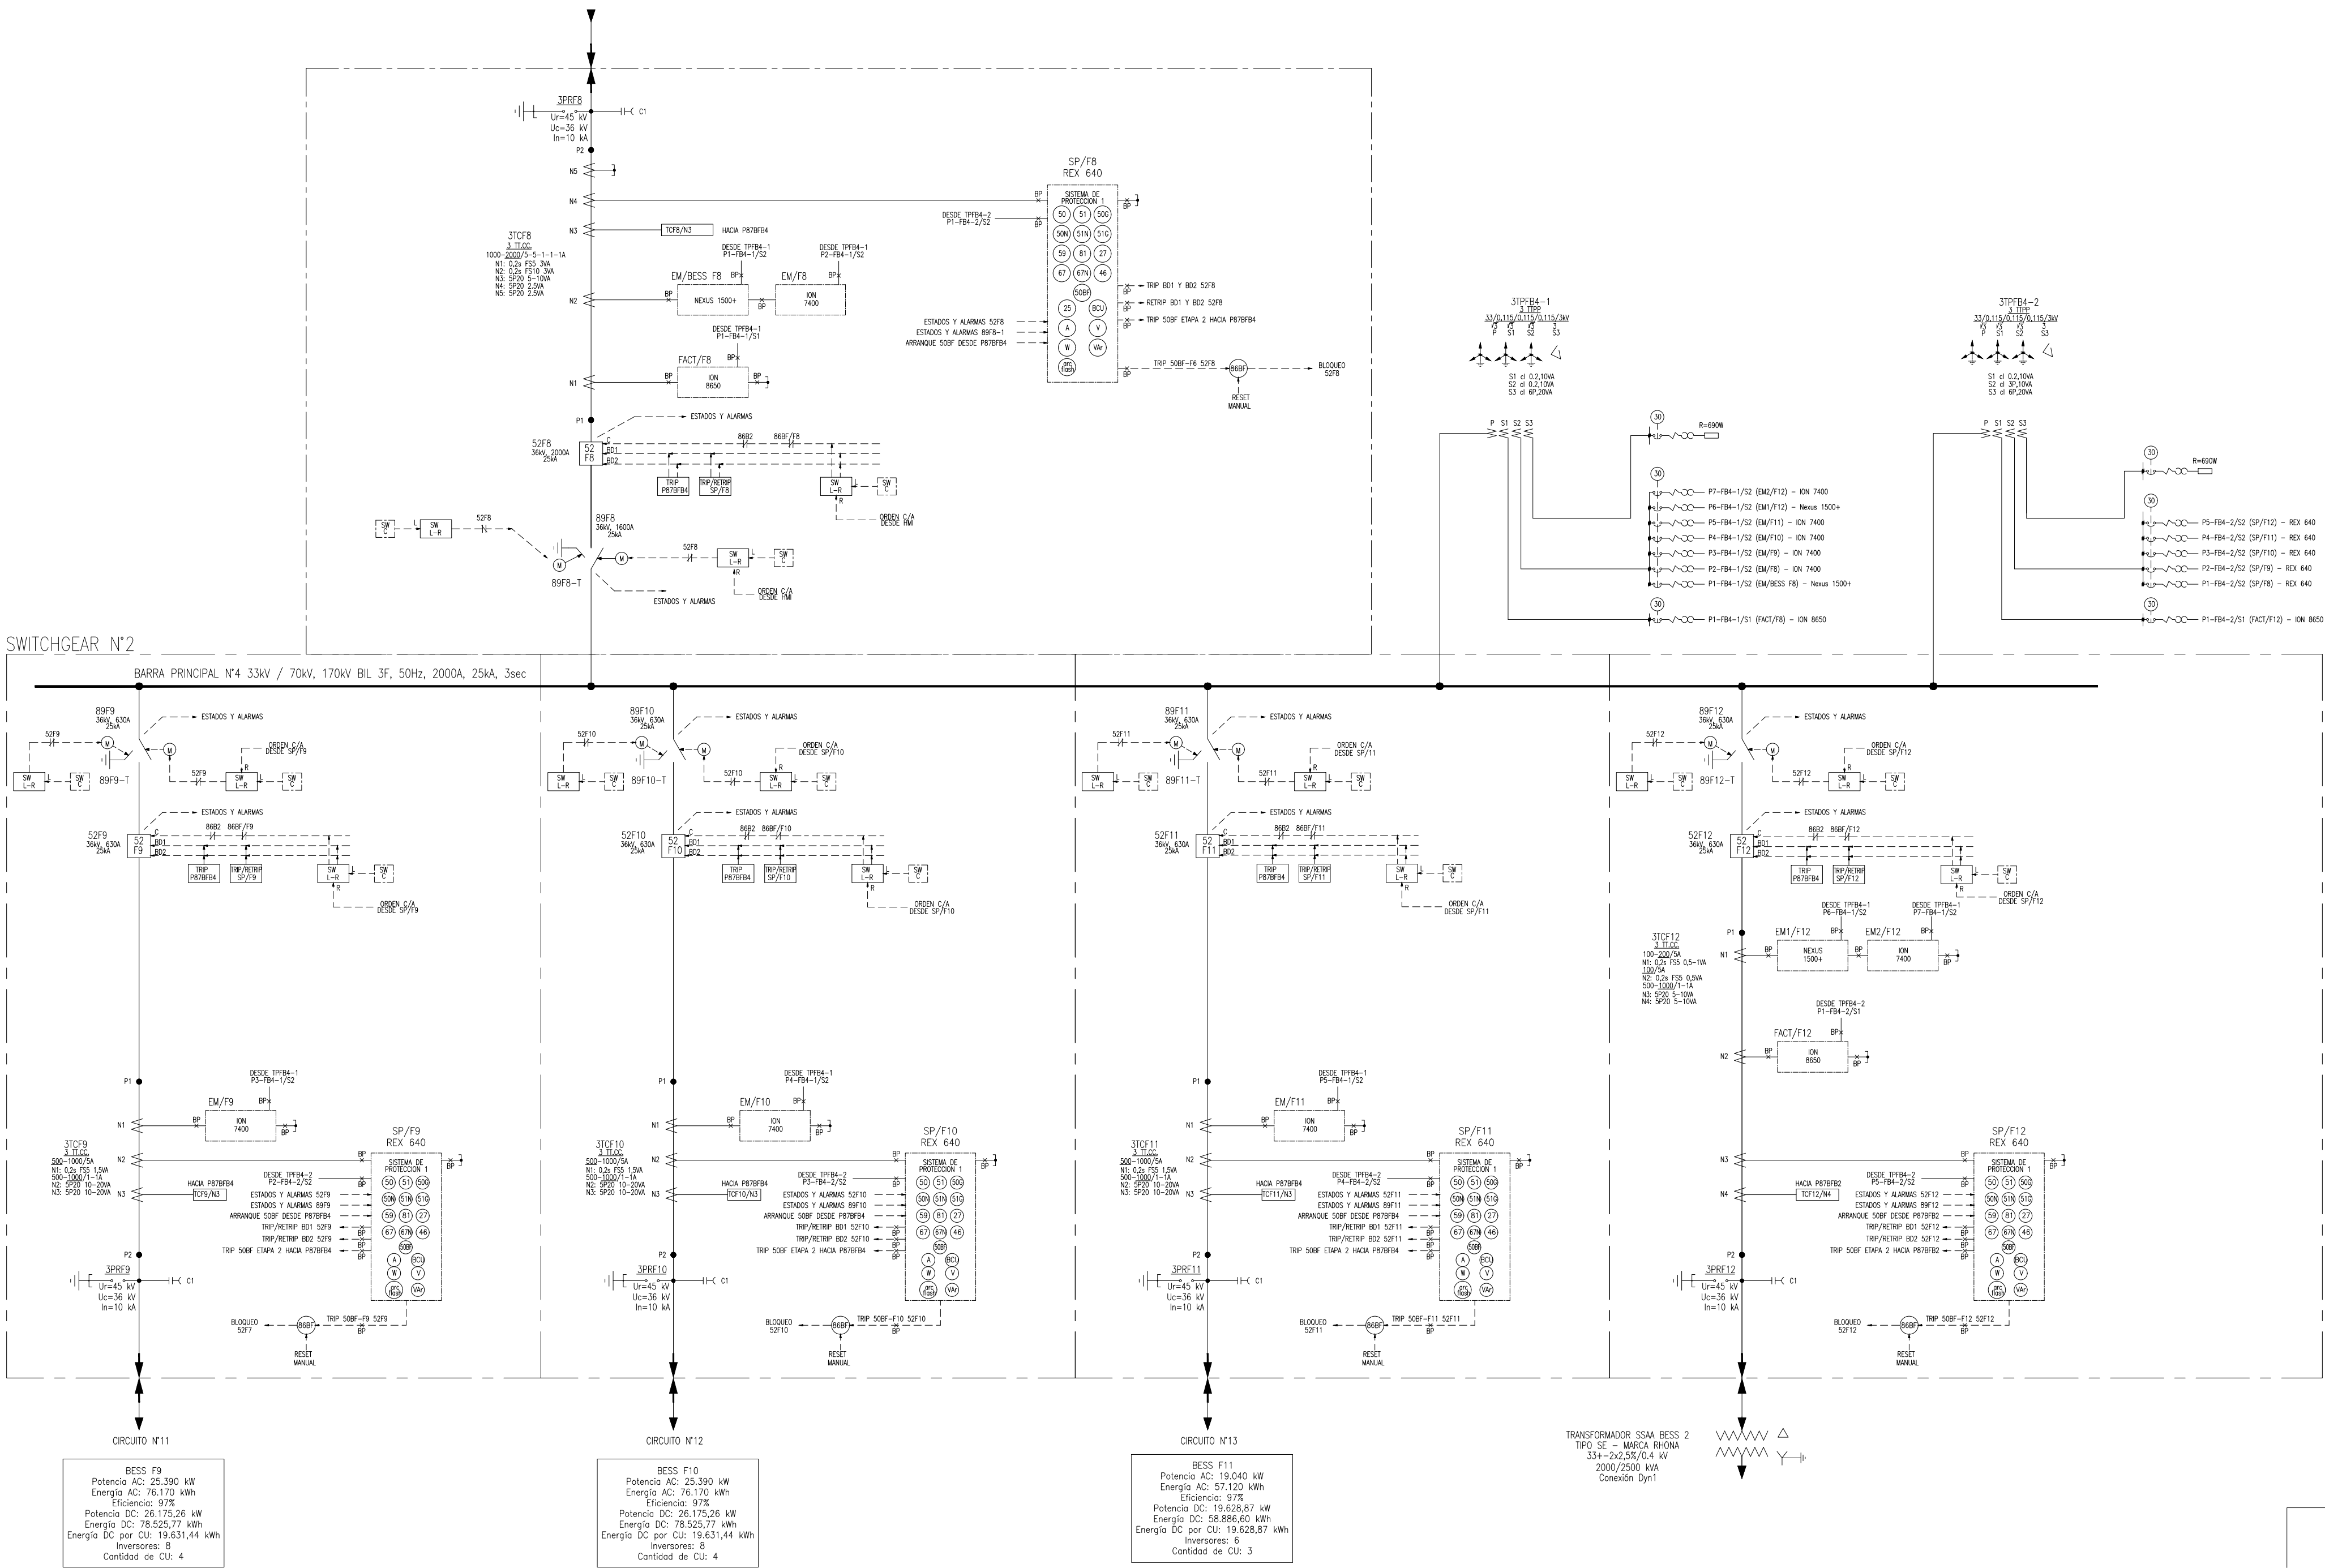

INGENIERÍA DE DETALLES PROYECTO BESS BOLERO



PLANO N°
23096-01-EE-DU-003

TÍTULO:
DIAGRAMA UNILINEAL
FUNCIONAL
BESS BOLERO 33kV
SWG 2

NORMA
REVISIÓN
ESCALA
LÁMINA 4 DE 4

DIBUJÓ	NOMBRE	FECHA
I-SEP	I-SEP	24.10.2024
PROYECTÓ	I-SEP	24.10.2024
REVISÓ	I-SEP	24.10.2024
APROBÓ	I-SEP	24.10.2024

REFERENCIA	PLANO/DOCUMENTO N°	DESCRIPCIÓN	REVISIÓN	FECHA	EMITIDO PARA USO	DESCRIPCIÓN
9	24.03.2025	ACTUALIZACIÓN	CEN			
8	18.03.2025	ACTUALIZACIÓN	CEN			
7	12.03.2025	ACTUALIZACIÓN	CEN			
6	11.02.2025	ACTUALIZACIÓN	CEN			
5	08.01.2025	ACTUALIZACIÓN	CEN			
4	27.12.2024	ACTUALIZACIÓN	CEN			
3	24.10.2024	ACTUALIZACIÓN	CEN			
2	12.04.2024	EMITIDO PARA USO				
1	15.01.2024	EMITIDO PARA USO				