


Validado para aprobación:


Plano verificado:

PLANO PARA APROBACIÓN



P.E. CAMPO LINDO. CIRCUITO 1

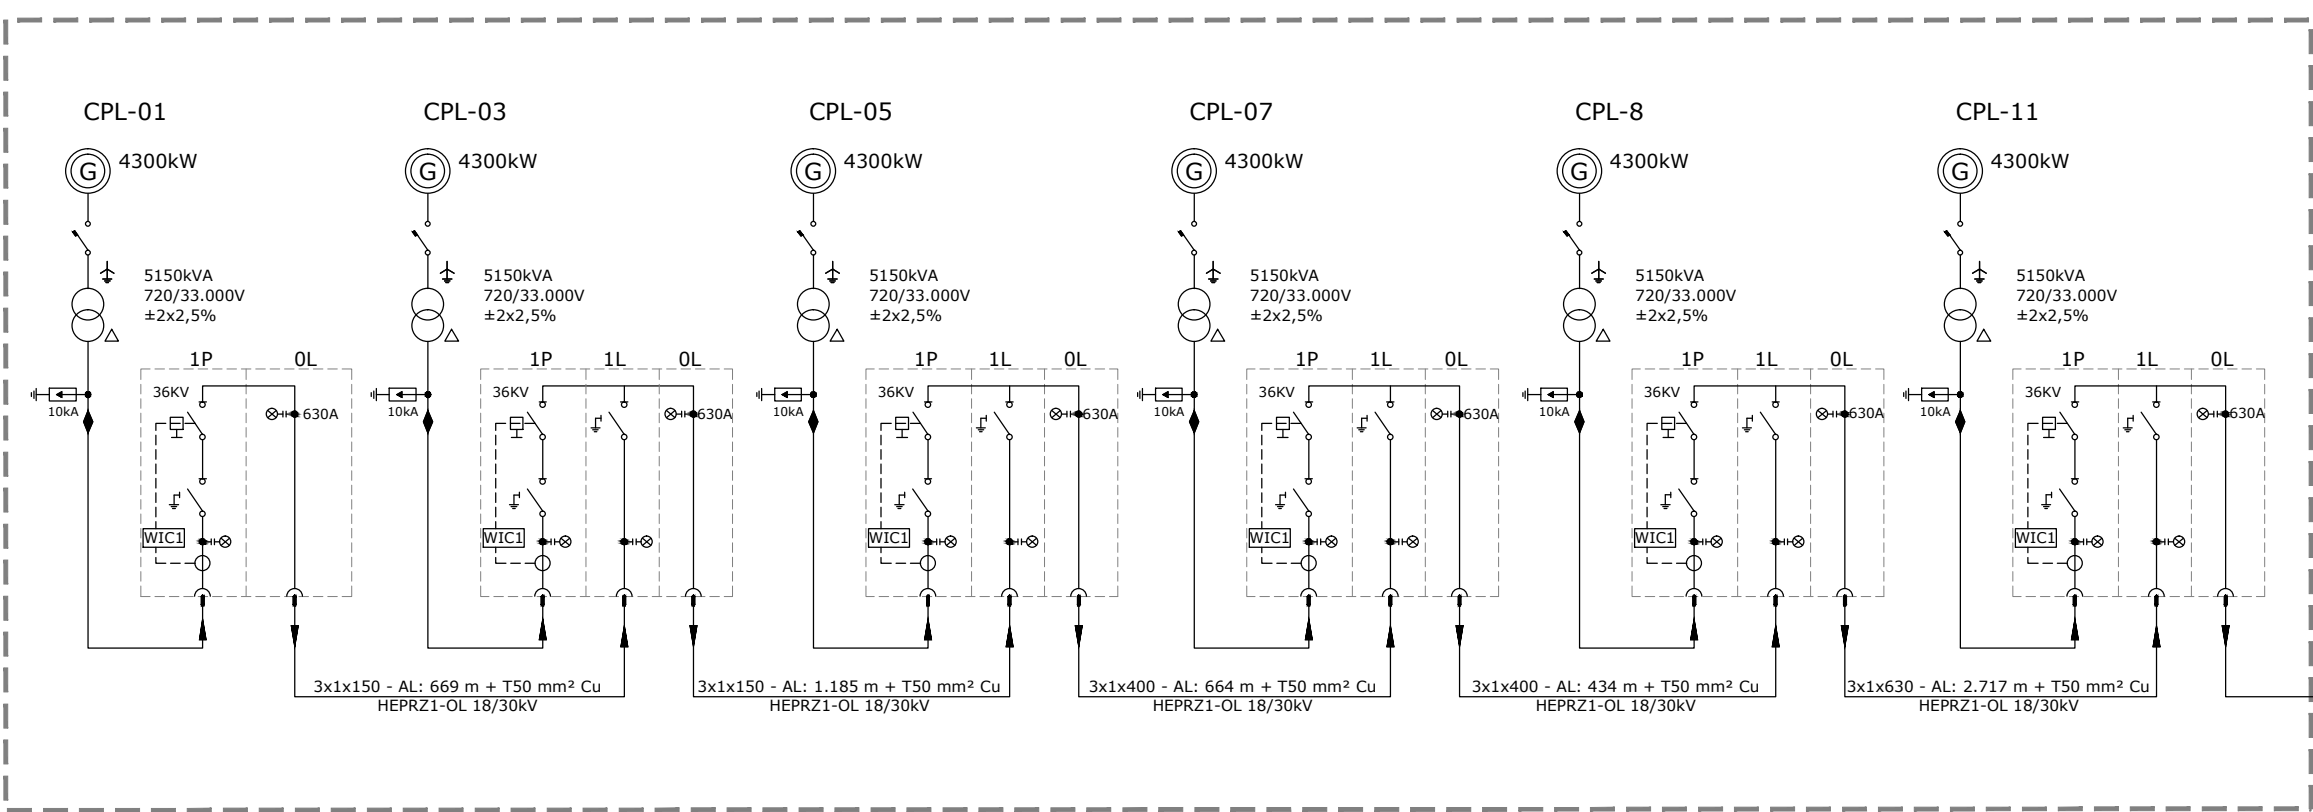

SUBESTACIÓN P.E. CAMPO LINDO (33/220kV)

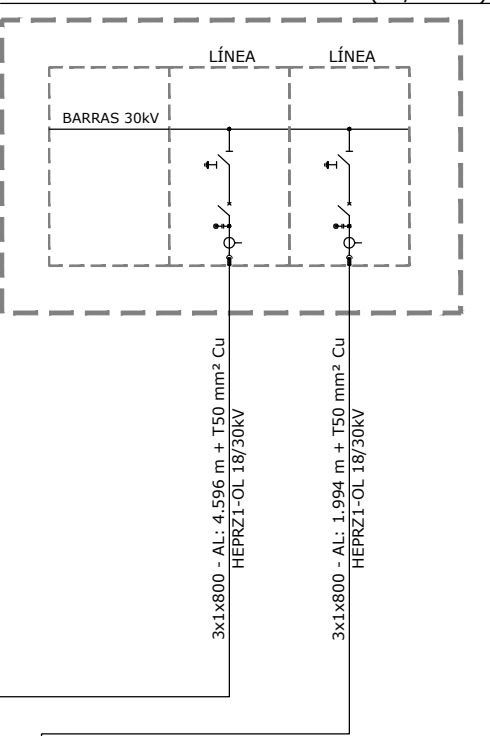

P.E. CAMPO LINDO. CIRCUITO 2

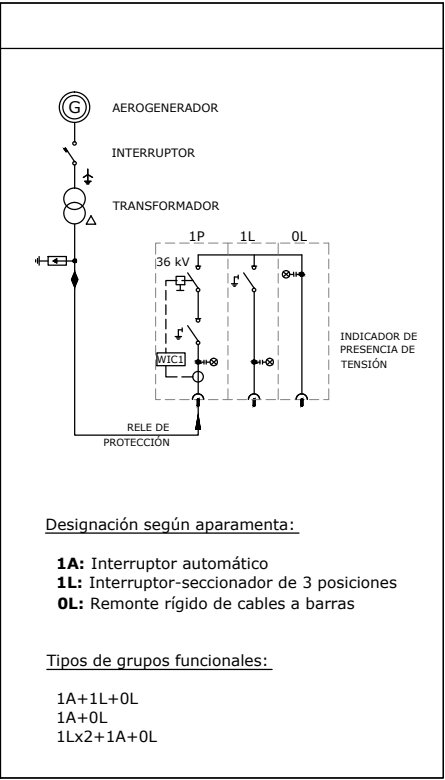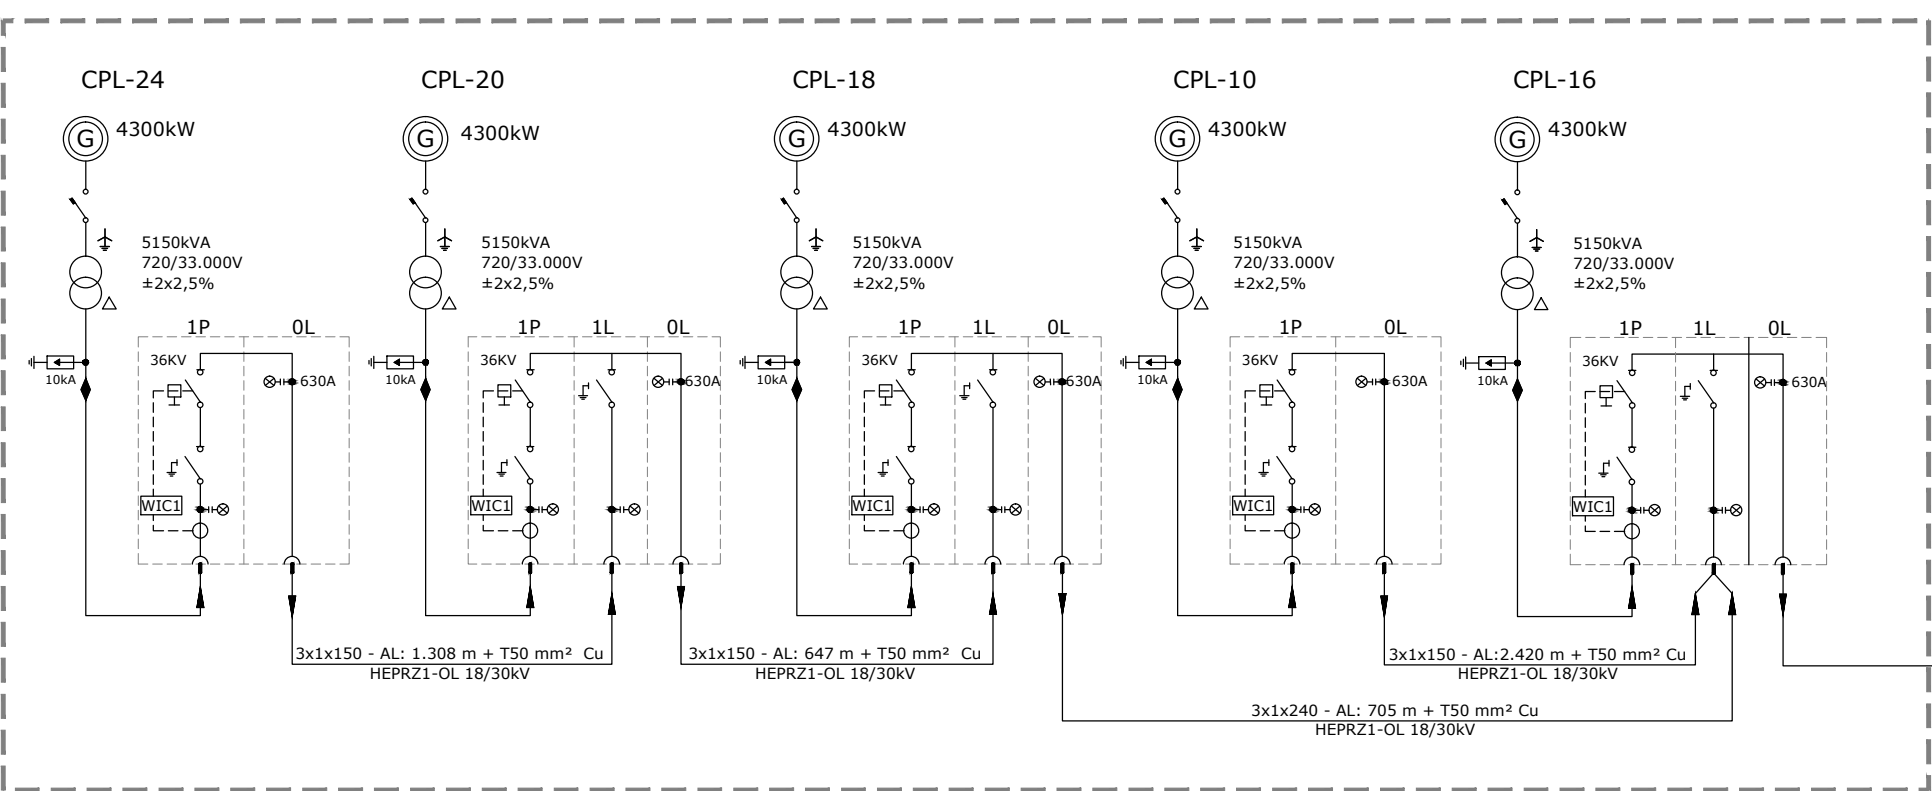

DOCUMENTOS DE REFERENCIA	
- OE-3-CAL-6-MC-01_ Memoria de cálculo - Red de media tensión	
- OE-3-CAL-6-DW-04_ RMT. Planta general y detalle	

7	21-11-22	A.O.L.	A.C.F.	G.D.S.	A.B.A.	ELIMINACIÓN CPL-13 Y CPL-09
6	29-04-22	A.O.L.	A.C.F.	G.D.S.	A.B.A.	NOTA CPL-13
5	28-04-22	A.O.L.	A.C.F.	G.D.S.	A.B.A.	INSTALACIÓN CPL-13
4	28-03-22	A.O.L.	A.C.F.	G.D.S.	A.B.A.	INSTALACIÓN FUTURA CPL-13
Rev.	Fecha	Proyect.	Dibujado	Comprob.	Aprobado	Modificación

SISTEMA COORDENADAS UTM WGS84 HUSO 18 S	
A3	DIMENSIONES: METROS (m)
ESCALA:	S/E

PARQUE EÓLICO CAMPO LINDO (CHILE)	
RED DE MEDIA TENSIÓN	
ESQUEMA UNIFILAR	


GLOBAL ENERGY SERVICES	
N° CAD: OE-3-CAL-6-DW-03	REV. 7
HOJA: 01	SIGUE: 02

Validado para aprobación:



Plano verificado:

PLANO PARA APROBACIÓN

P.E. CAMPO LINDO. CIRCUITO 3

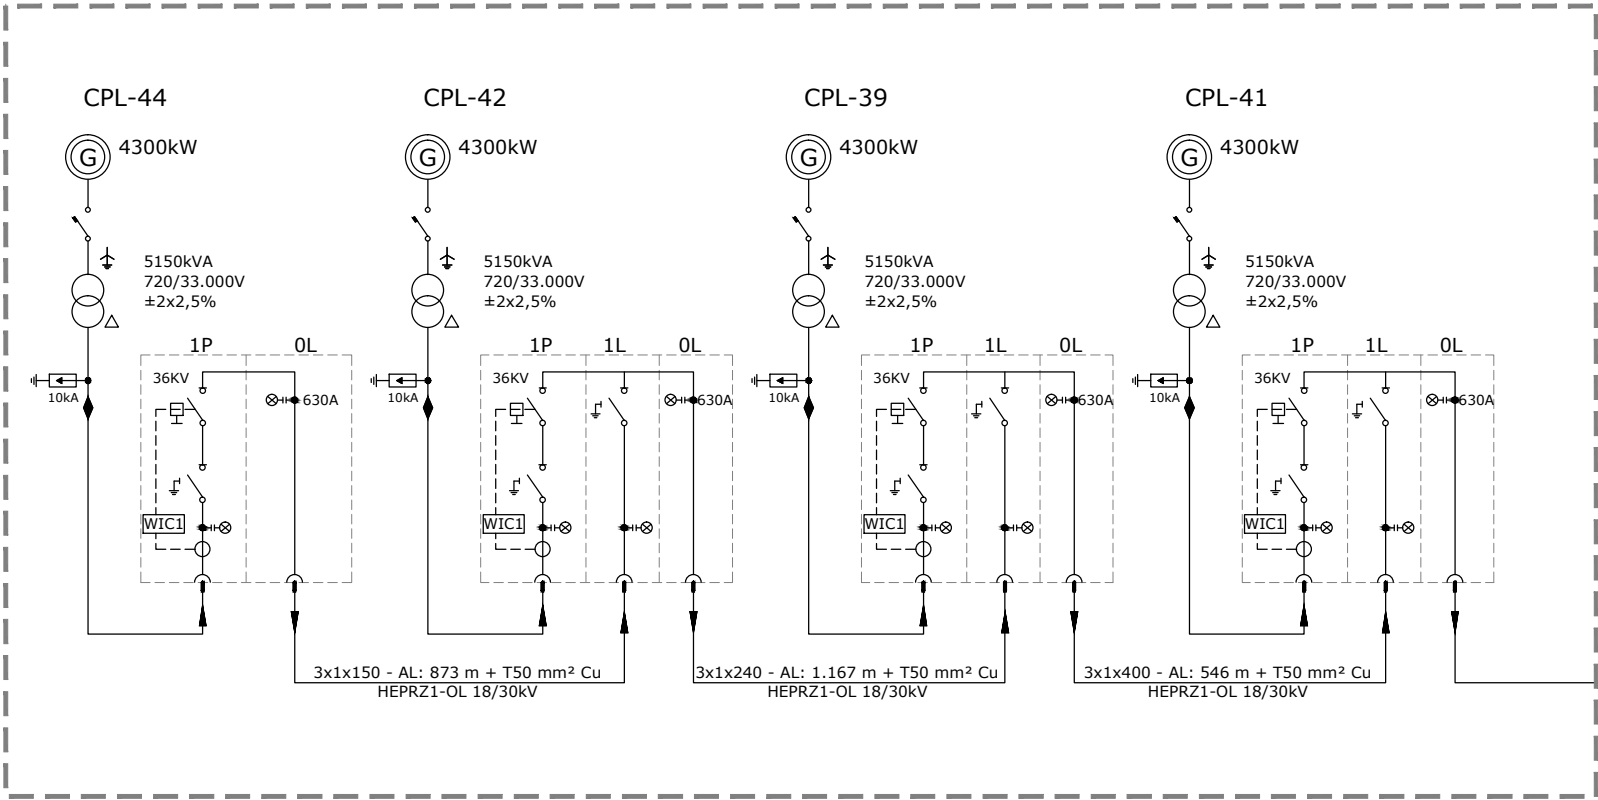

SUBESTACIÓN P.E. CAMPO LINDO (33/220kV)

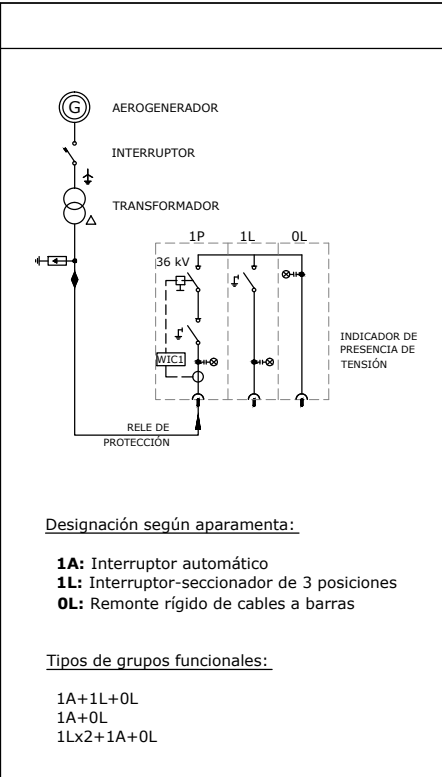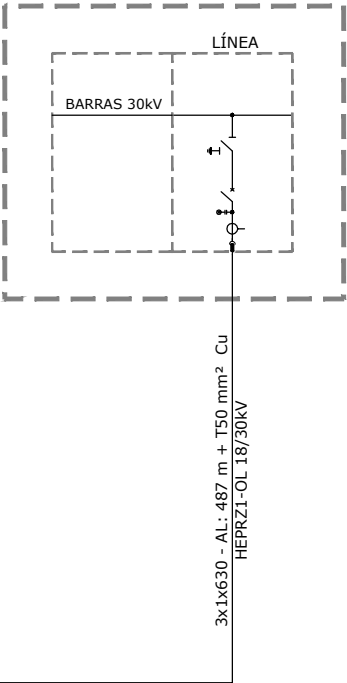

DOCUMENTOS DE REFERENCIA	
-	OE-3-CAL-6-MC-01_Memoria de cálculo - Red de media tensión
-	OE-3-CAL-6-DW-04_RMT. Planta general y detalle

7	21-11-22	A.O.L.	A.C.F.	G.D.S.	A.B.A.	ELIMINACIÓN CPL-13 Y CPL-09
6	29-04-22	A.O.L.	A.C.F.	G.D.S.	A.B.A.	NOTA CPL-13
5	28-04-22	A.O.L.	A.C.F.	G.D.S.	A.B.A.	INSTALACIÓN CPL-13
4	28-03-22	A.O.L.	A.C.F.	G.D.S.	A.B.A.	INSTALACIÓN FUTURA CPL-13
Rev.	Fecha	Proyect.	Dibujado	Comprob.	Aprobado	Modificación

SISTEMA COORDENADAS UTM WGS84 HUSO 18 S	
A3	DIMENSIONES: METROS (m)
ESCALA:	S/E

PARQUE EÓLICO CAMPO LINDO (CHILE)	
RED DE MEDIA TENSIÓN ESQUEMA UNIFILAR	

GLOBAL ENERGY SERVICES	
N° CAD: OE-3-CAL-6-DW-03	REV. 7
HOJA: 02	SIGUE: /