
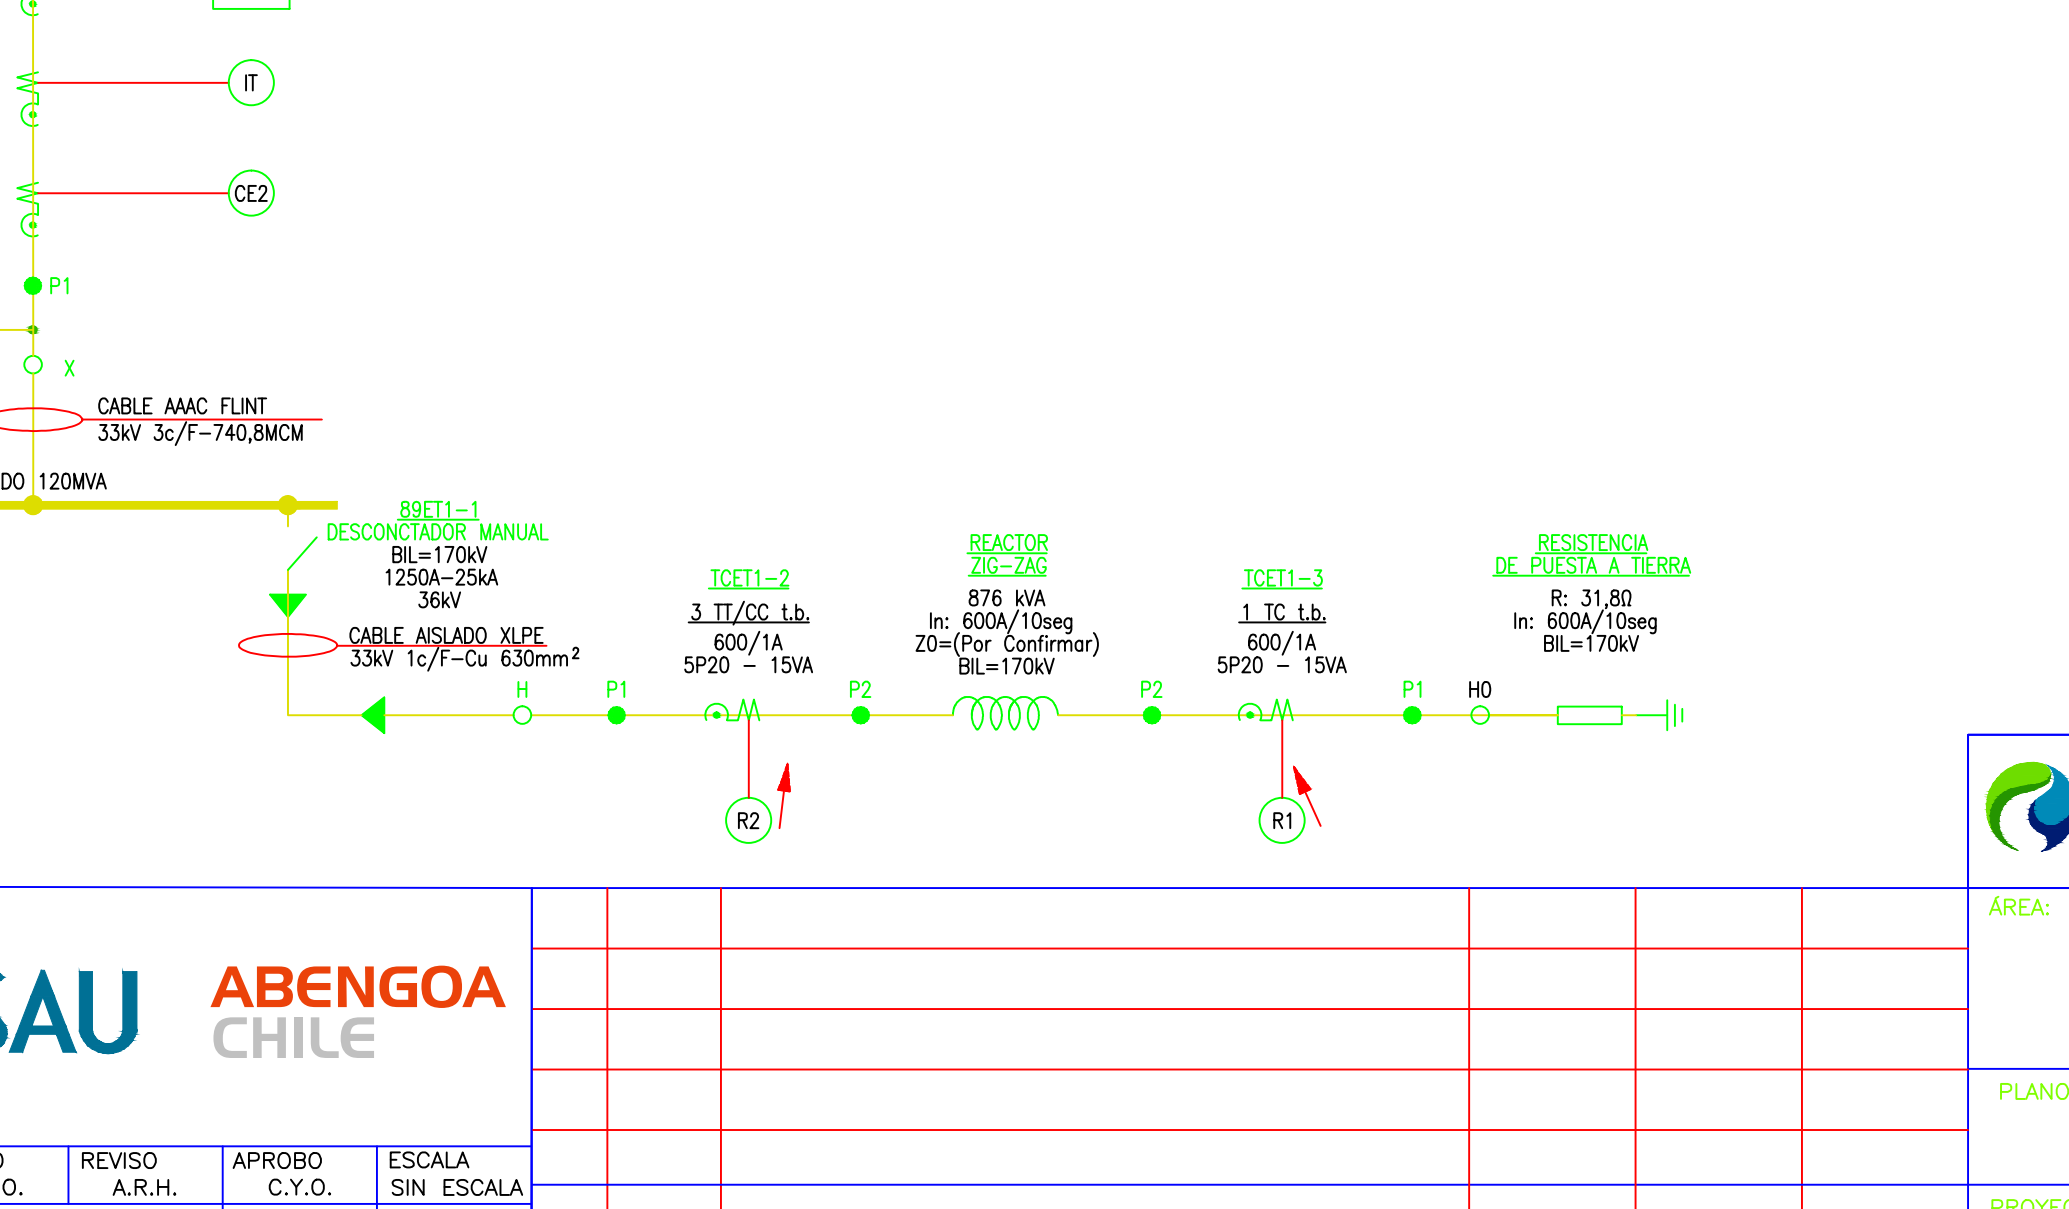
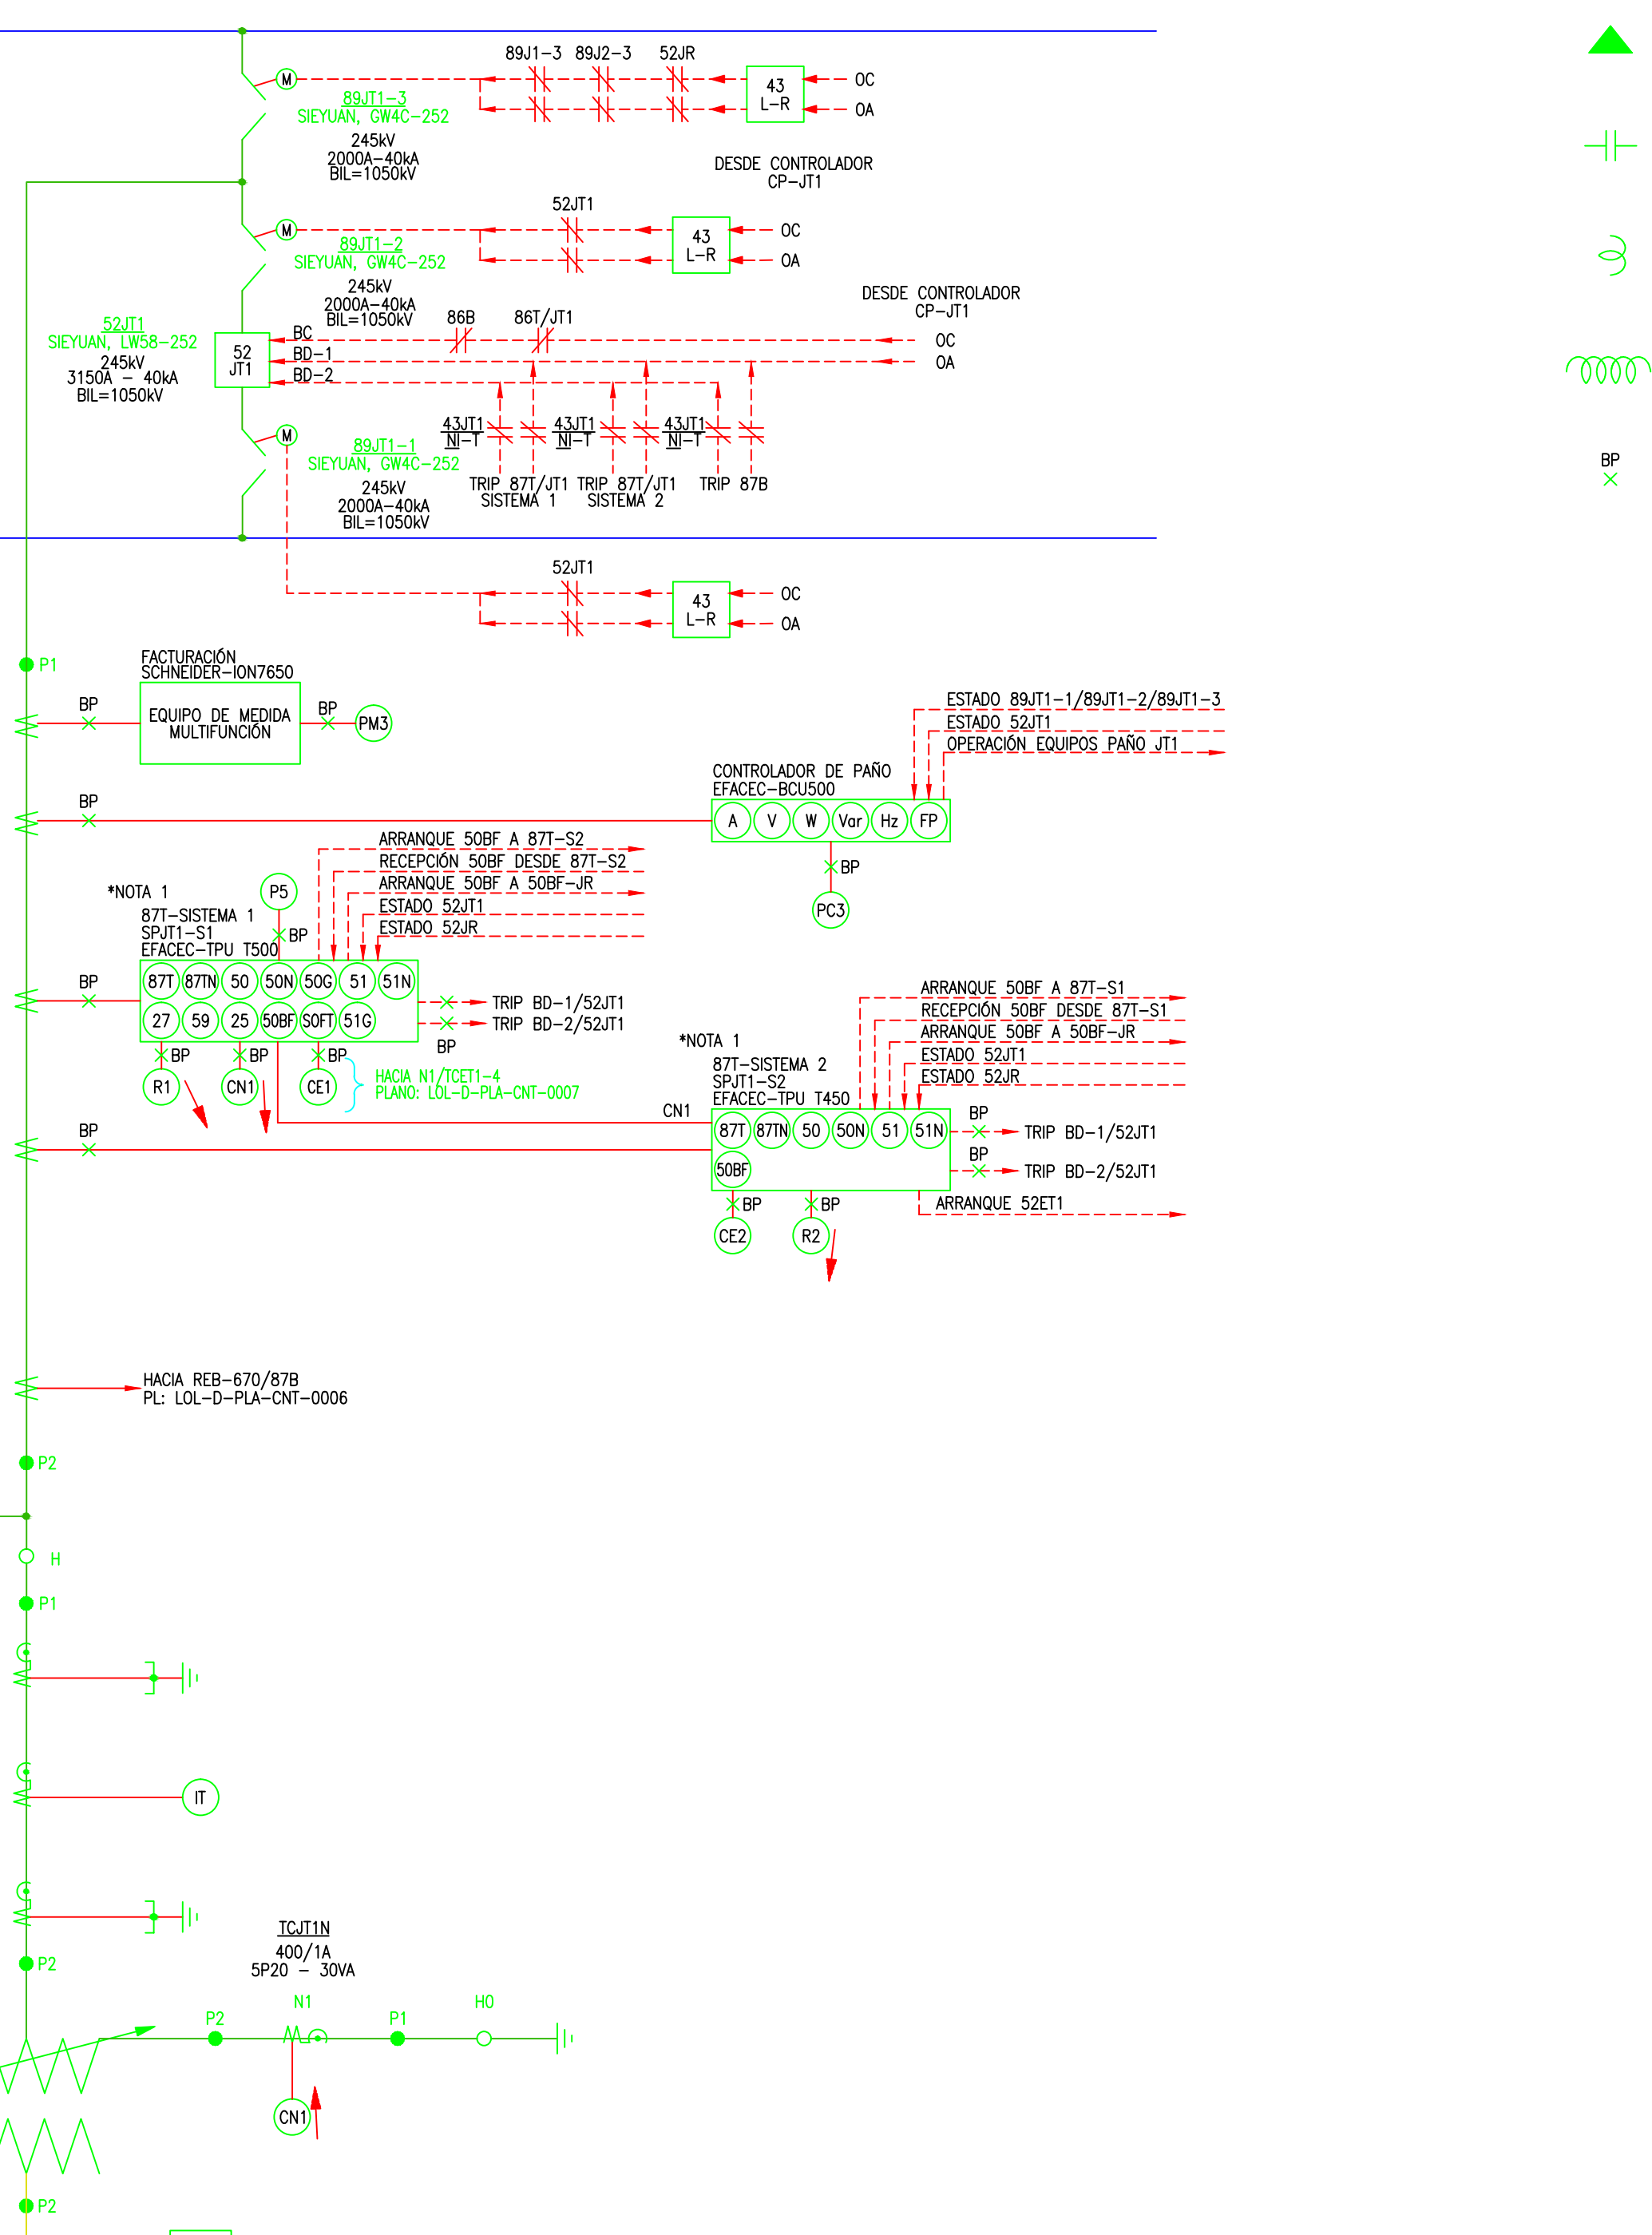
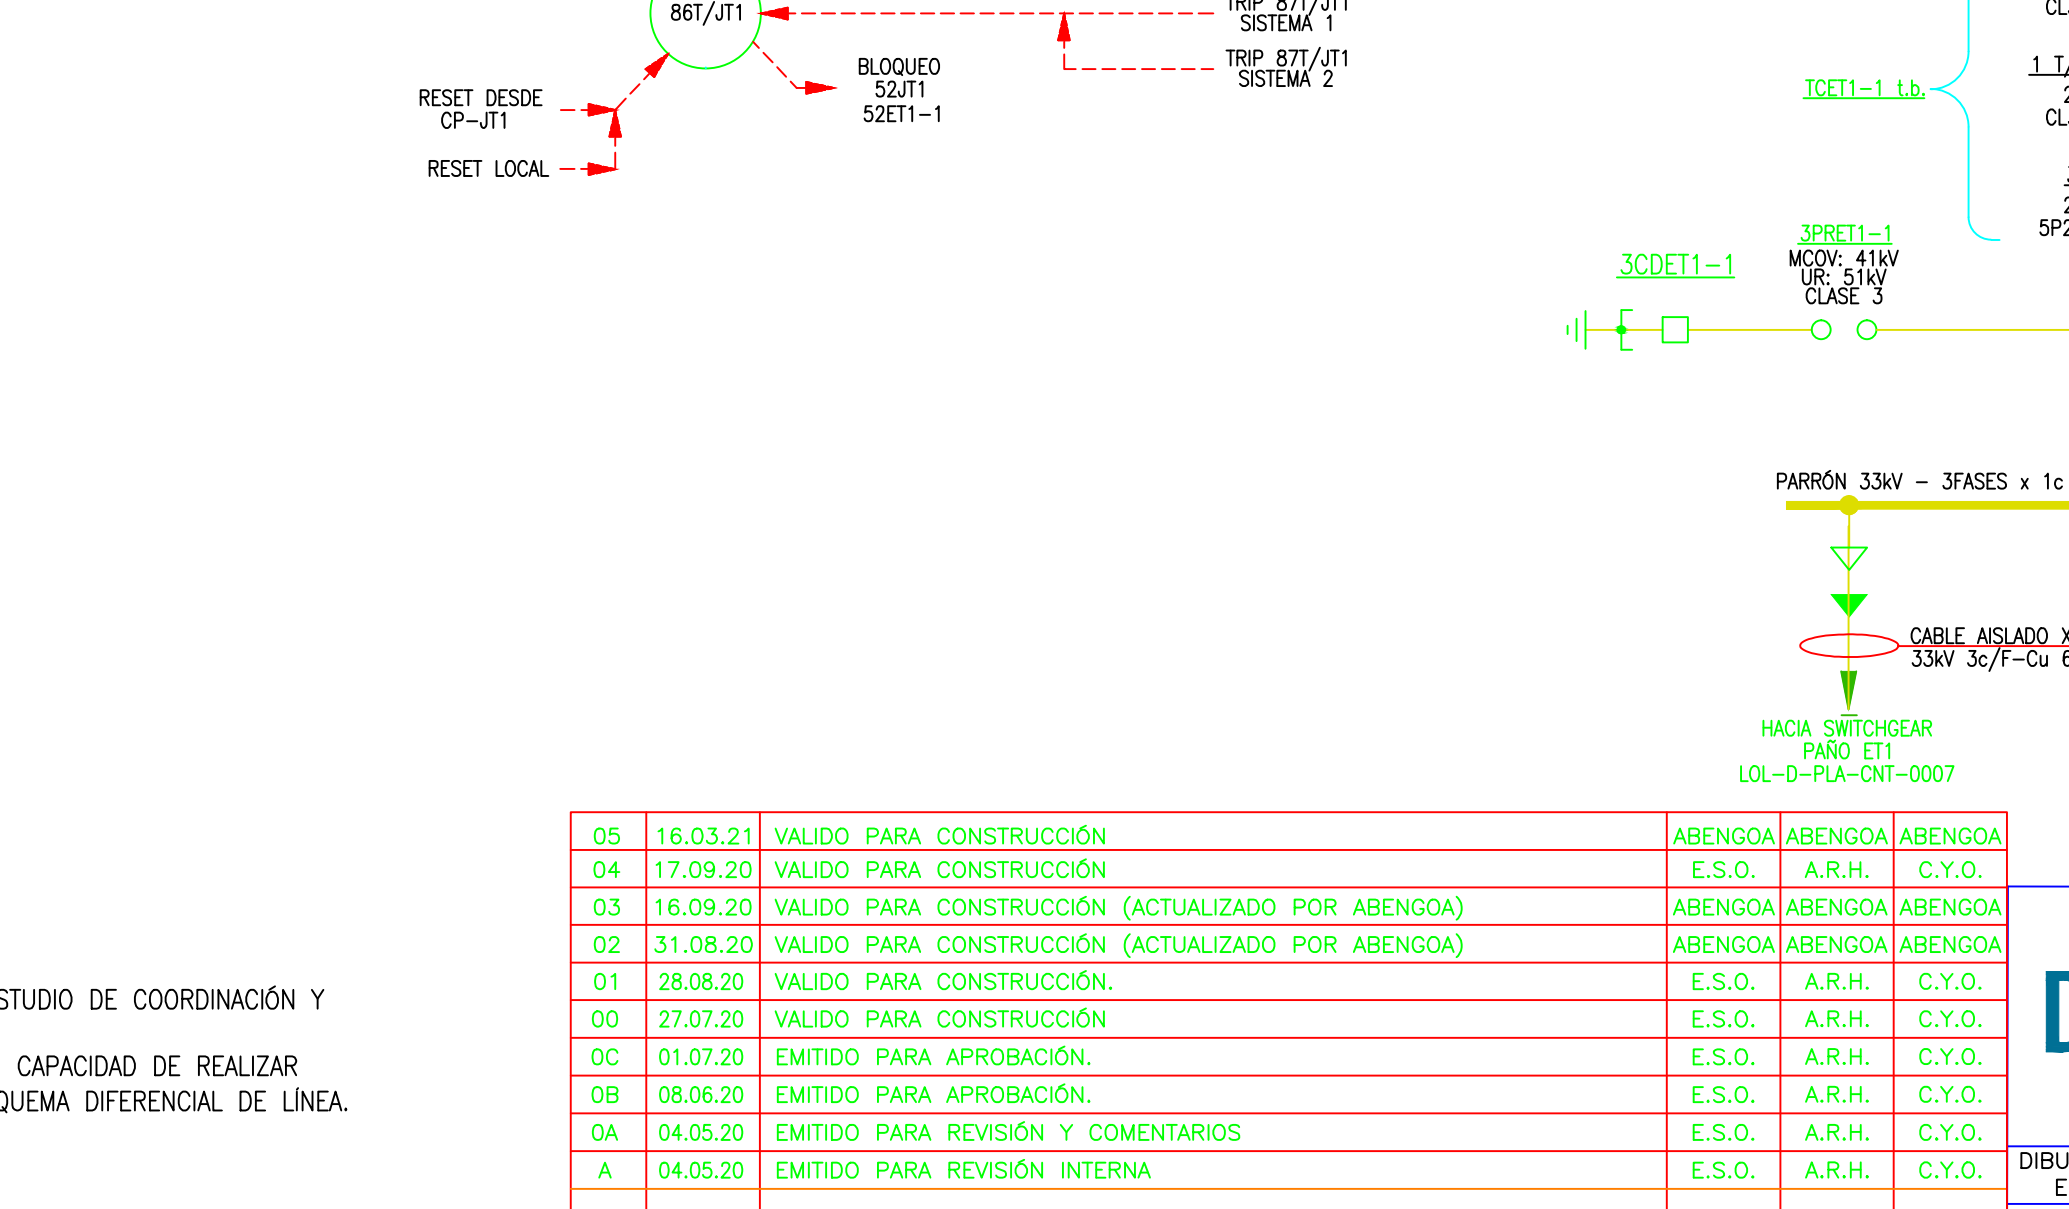
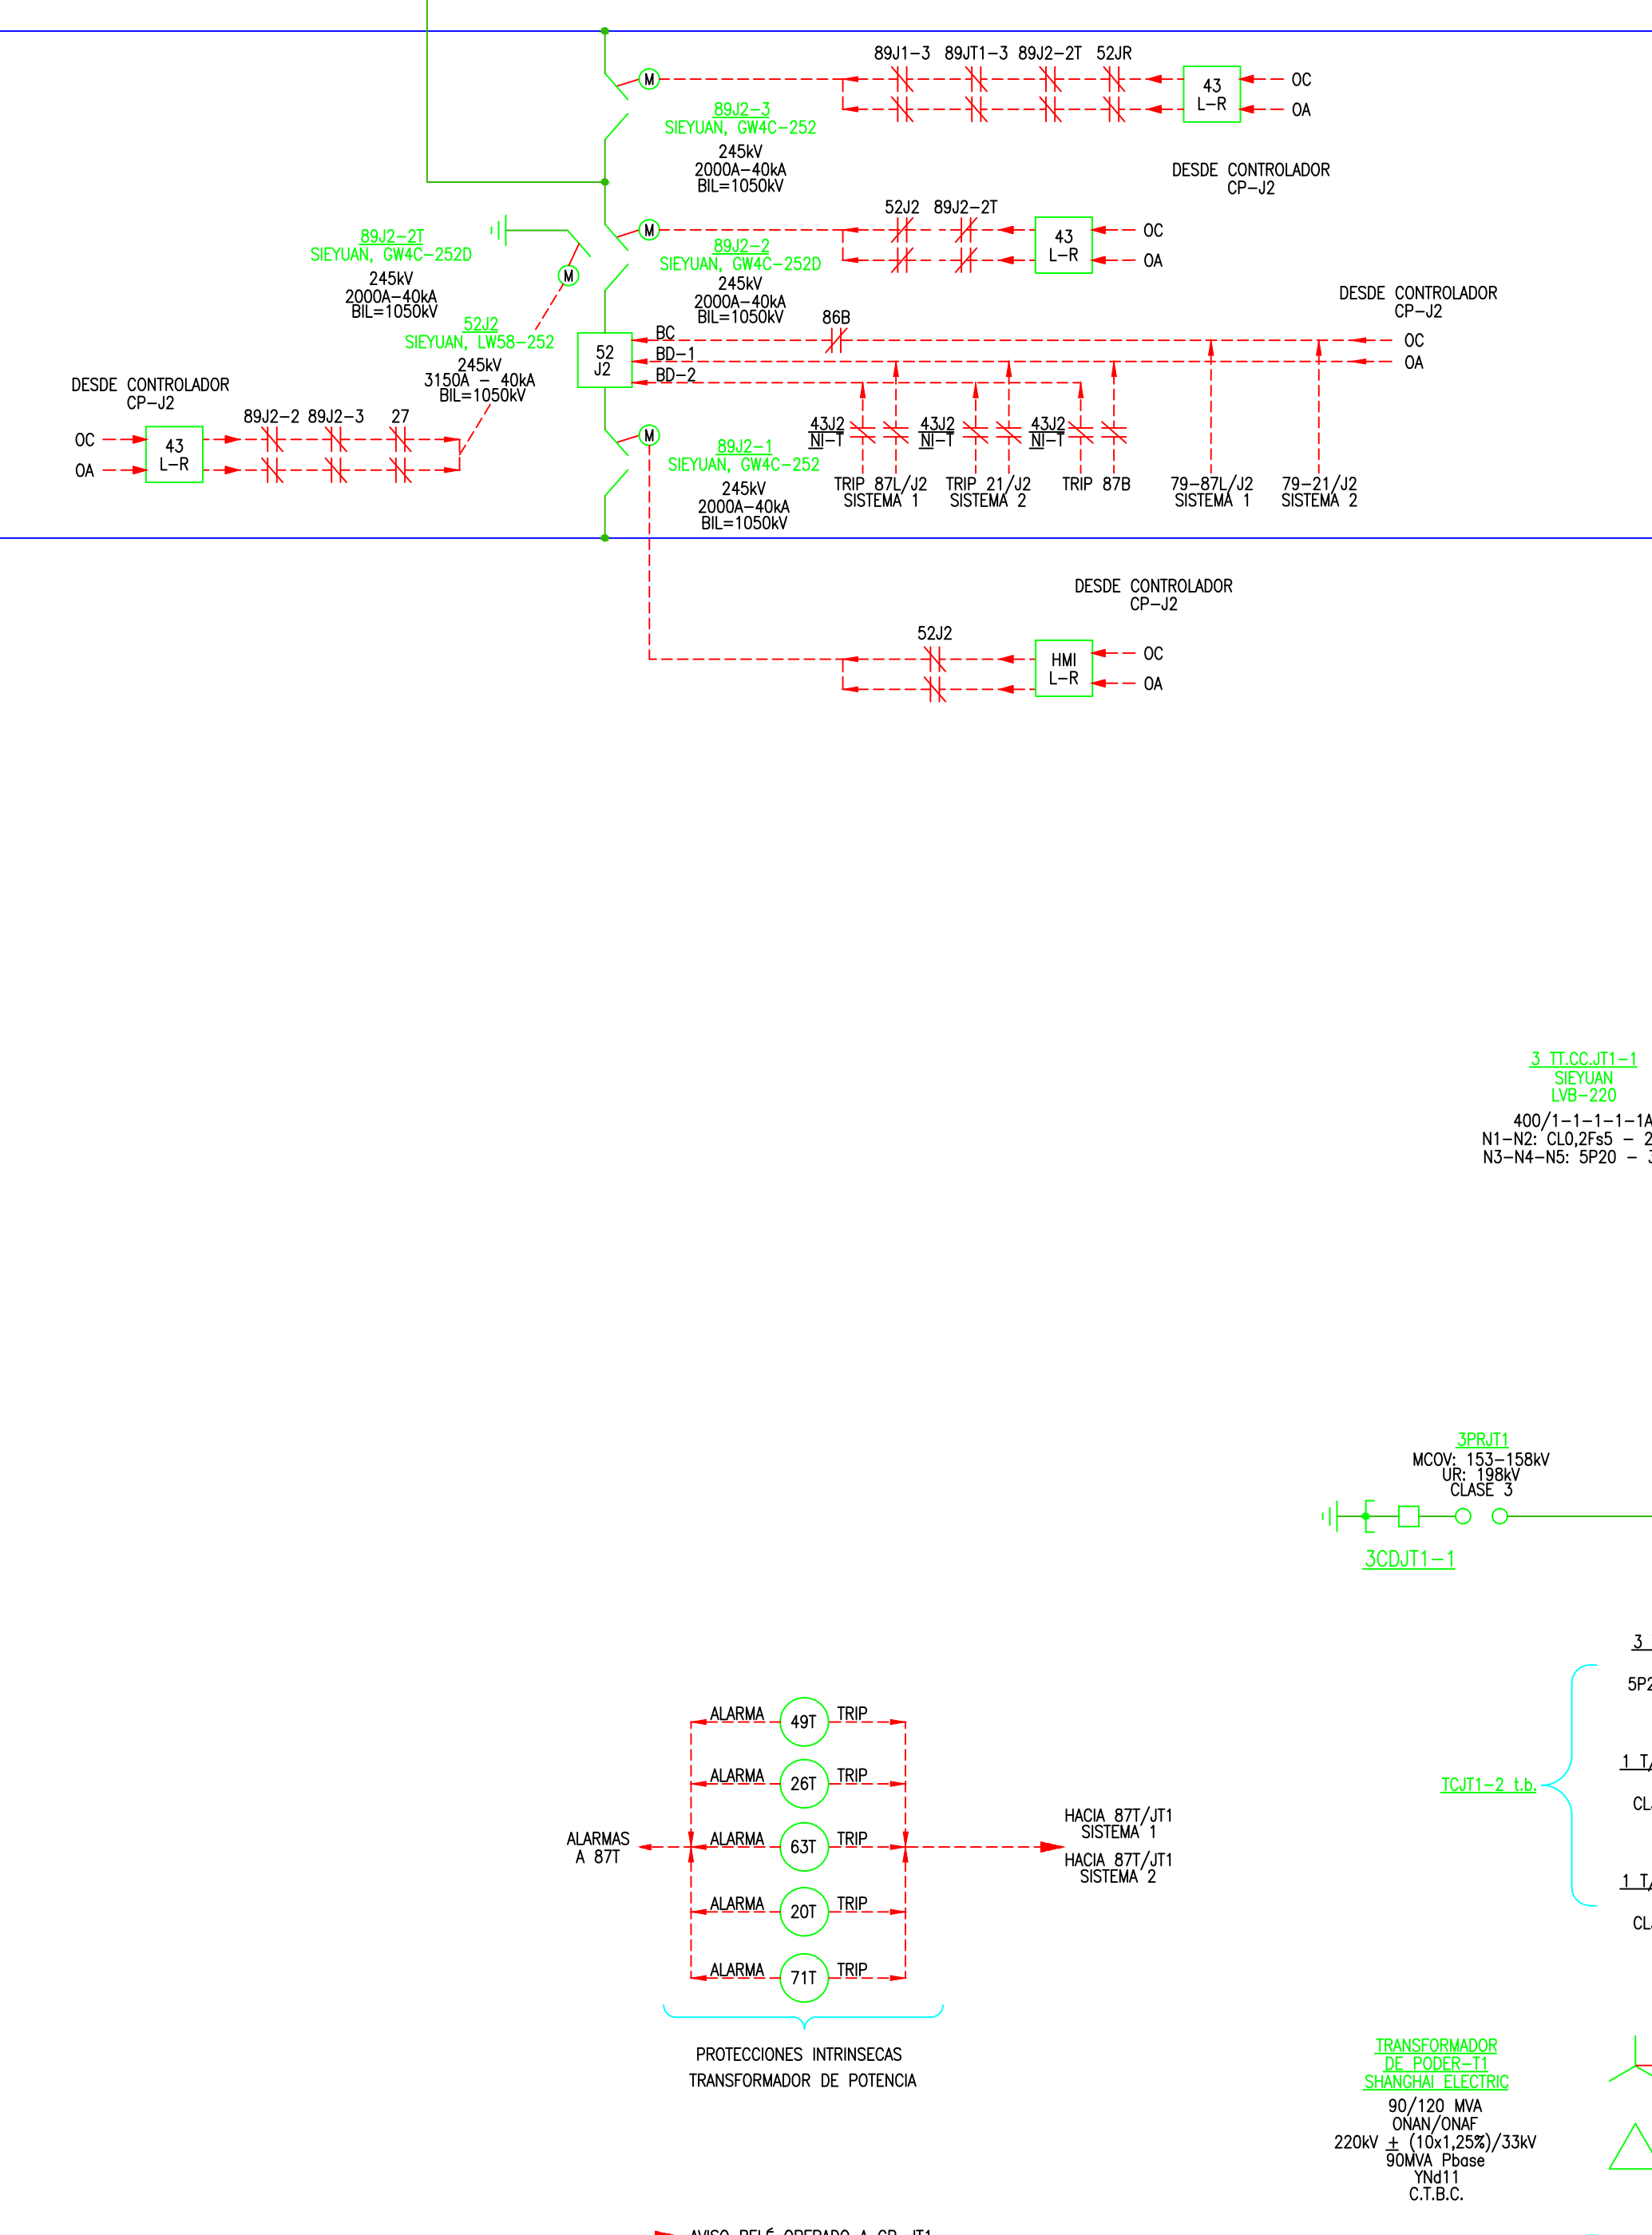
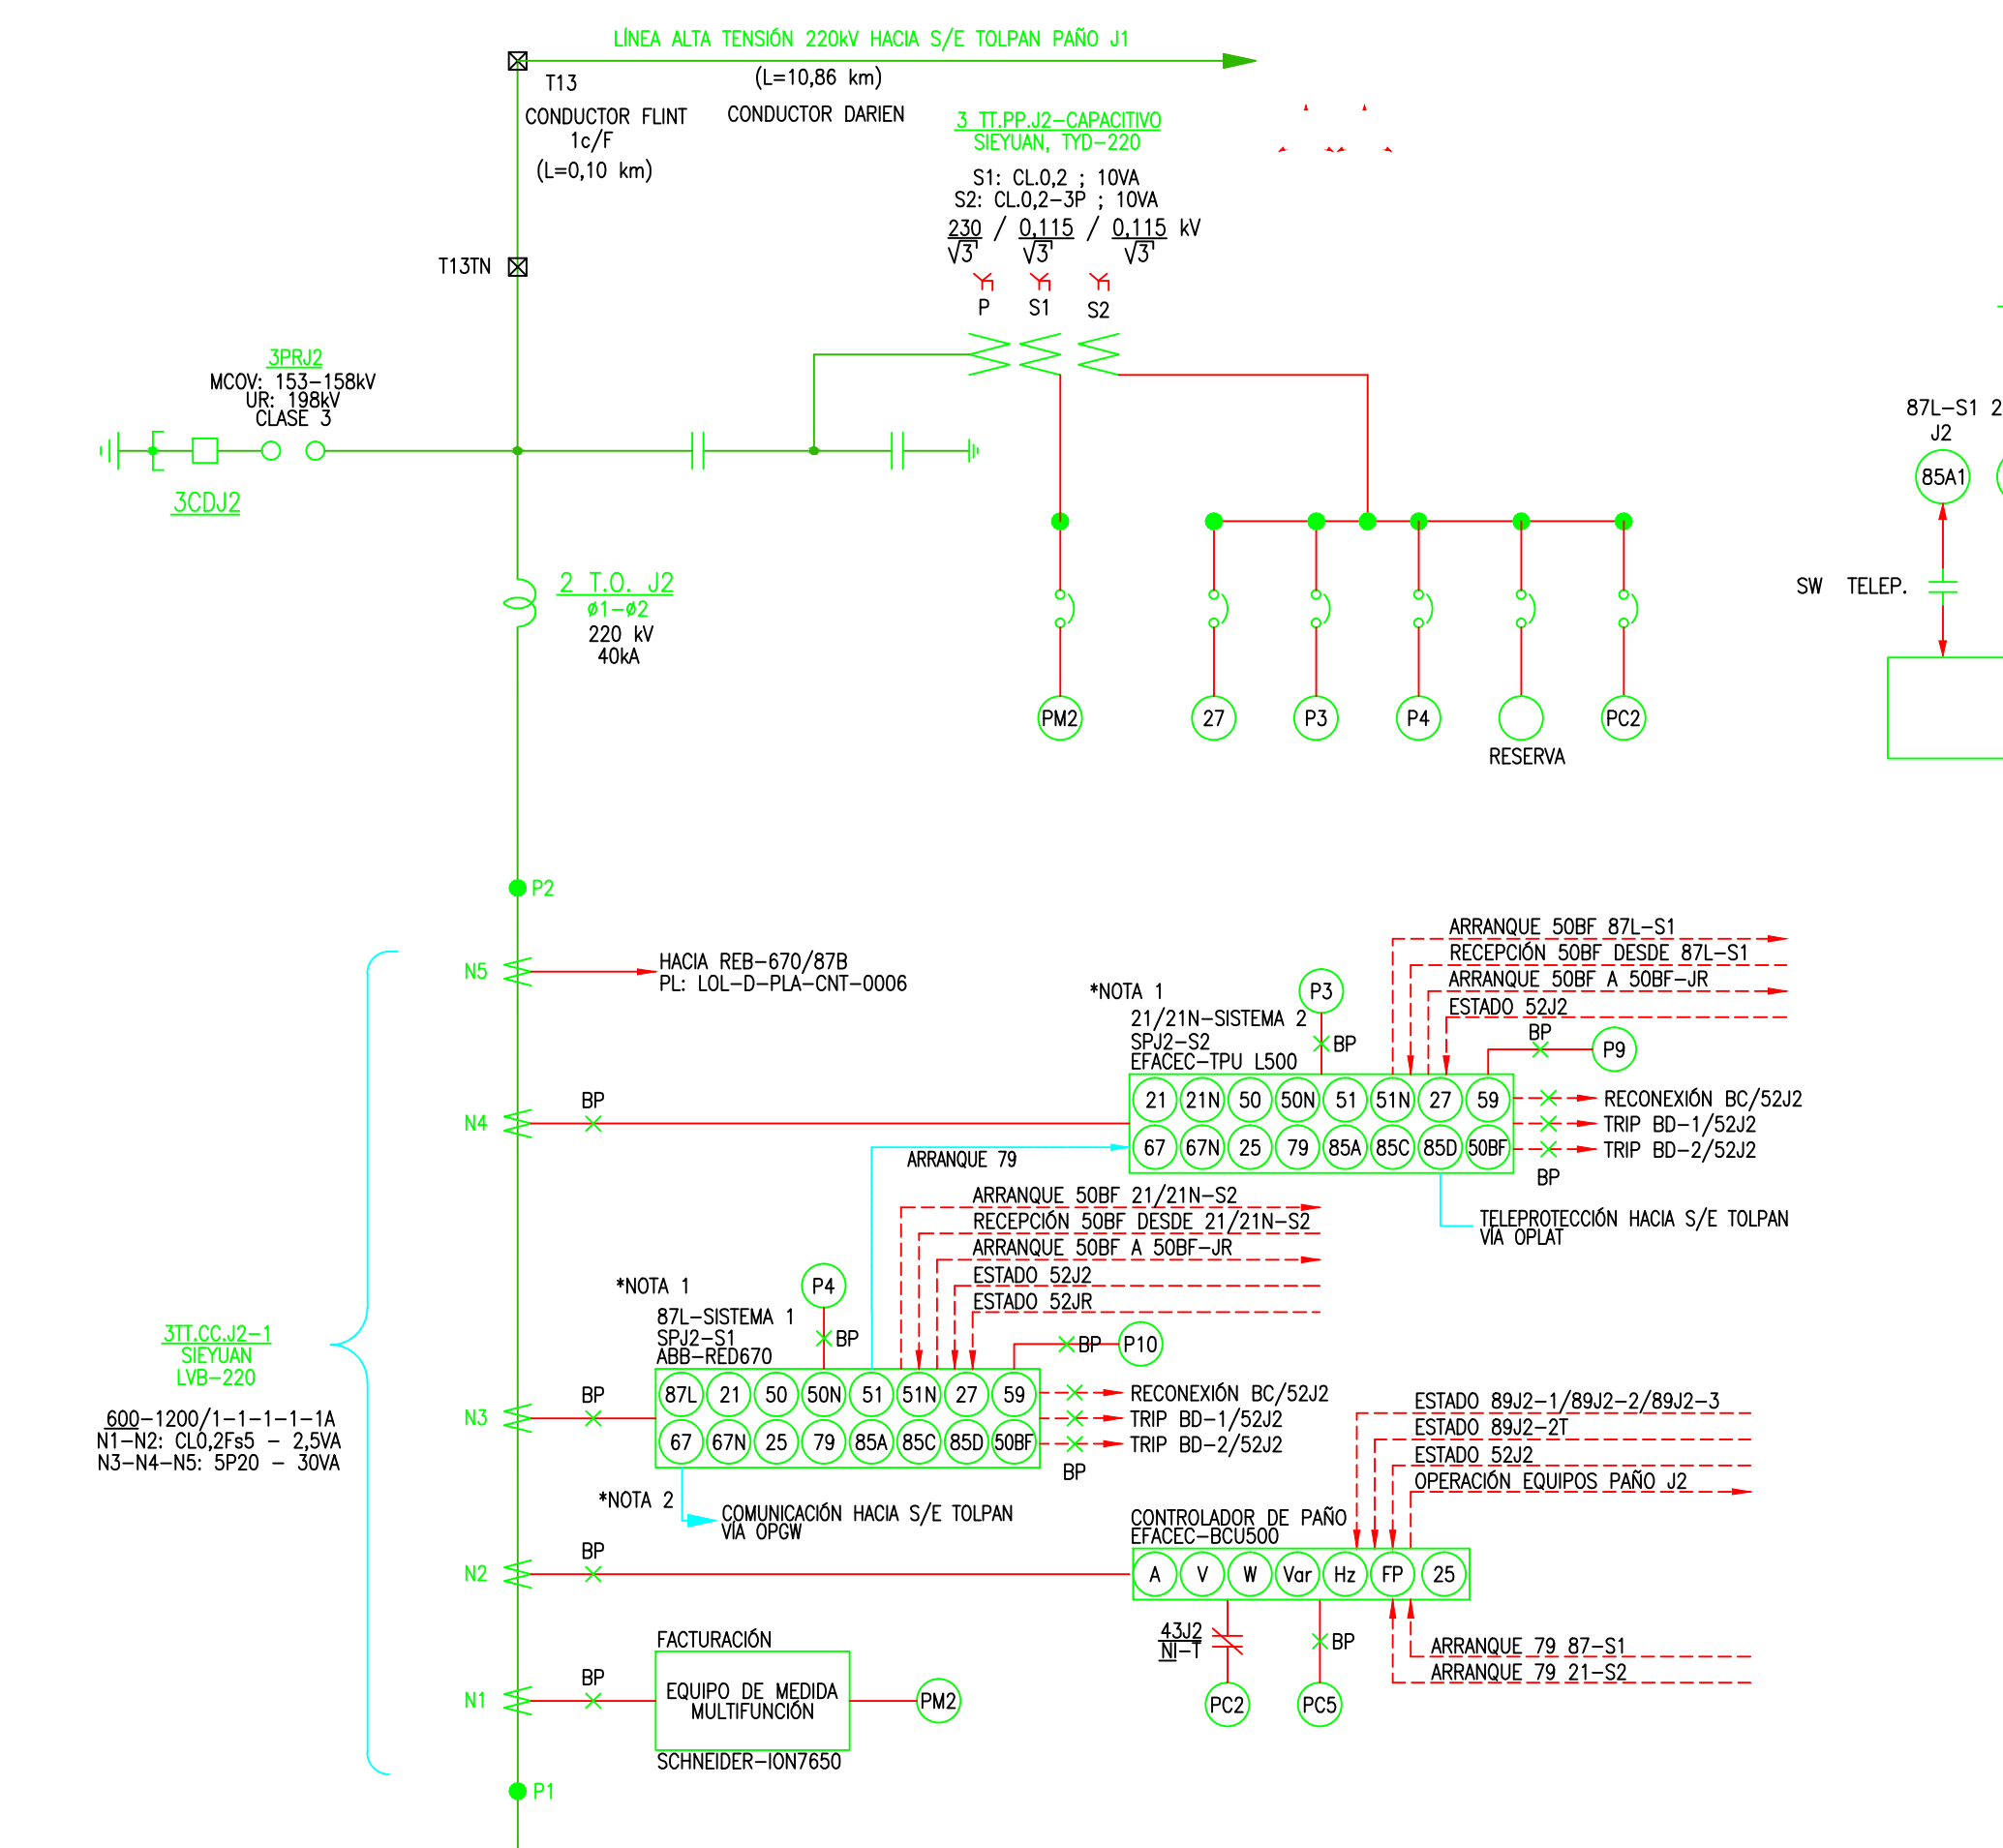
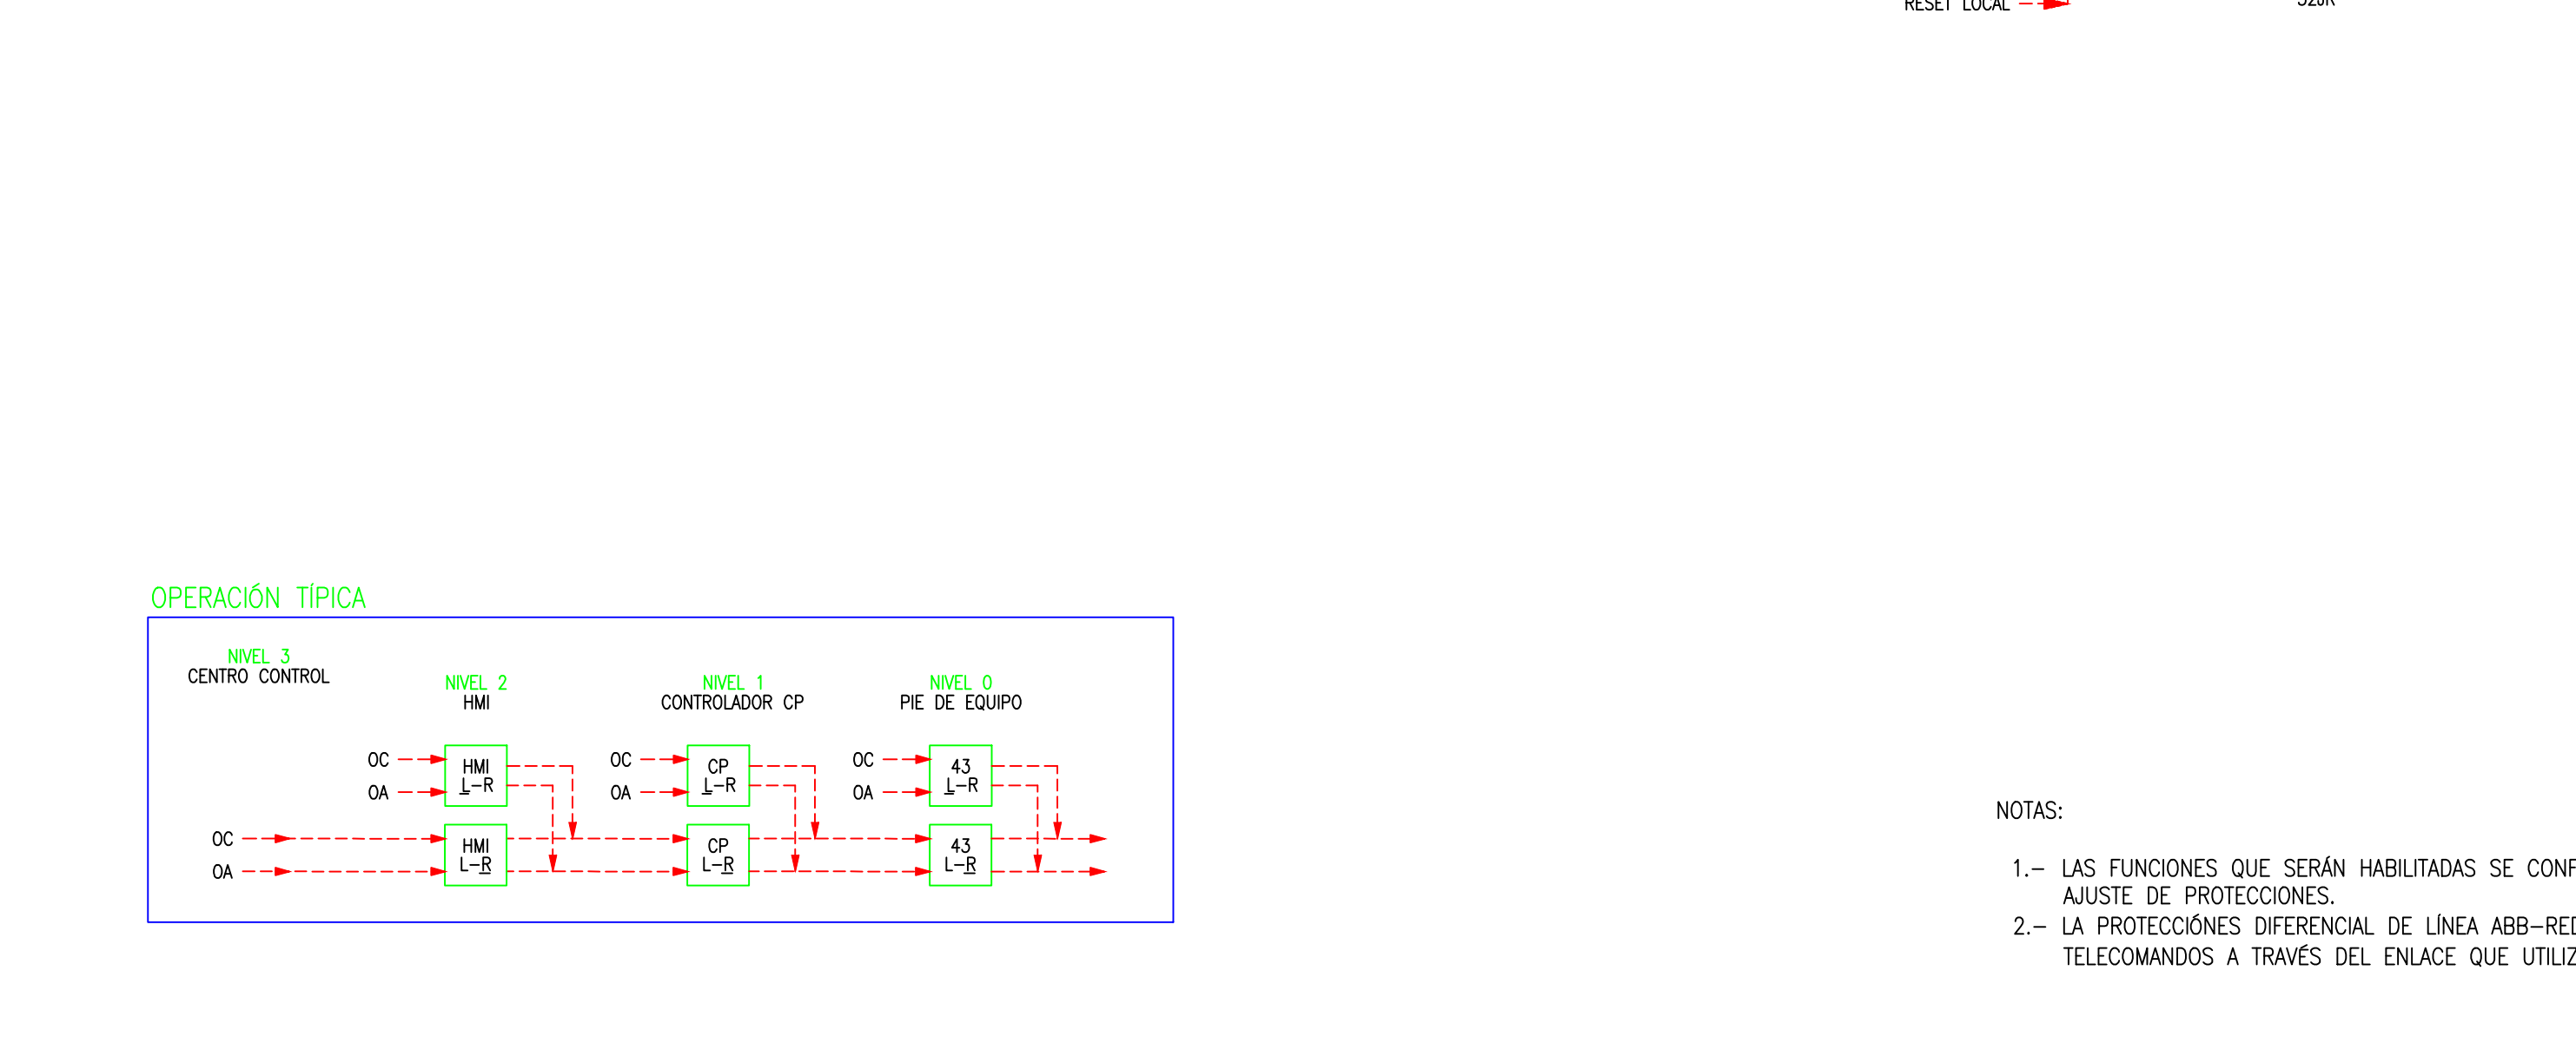
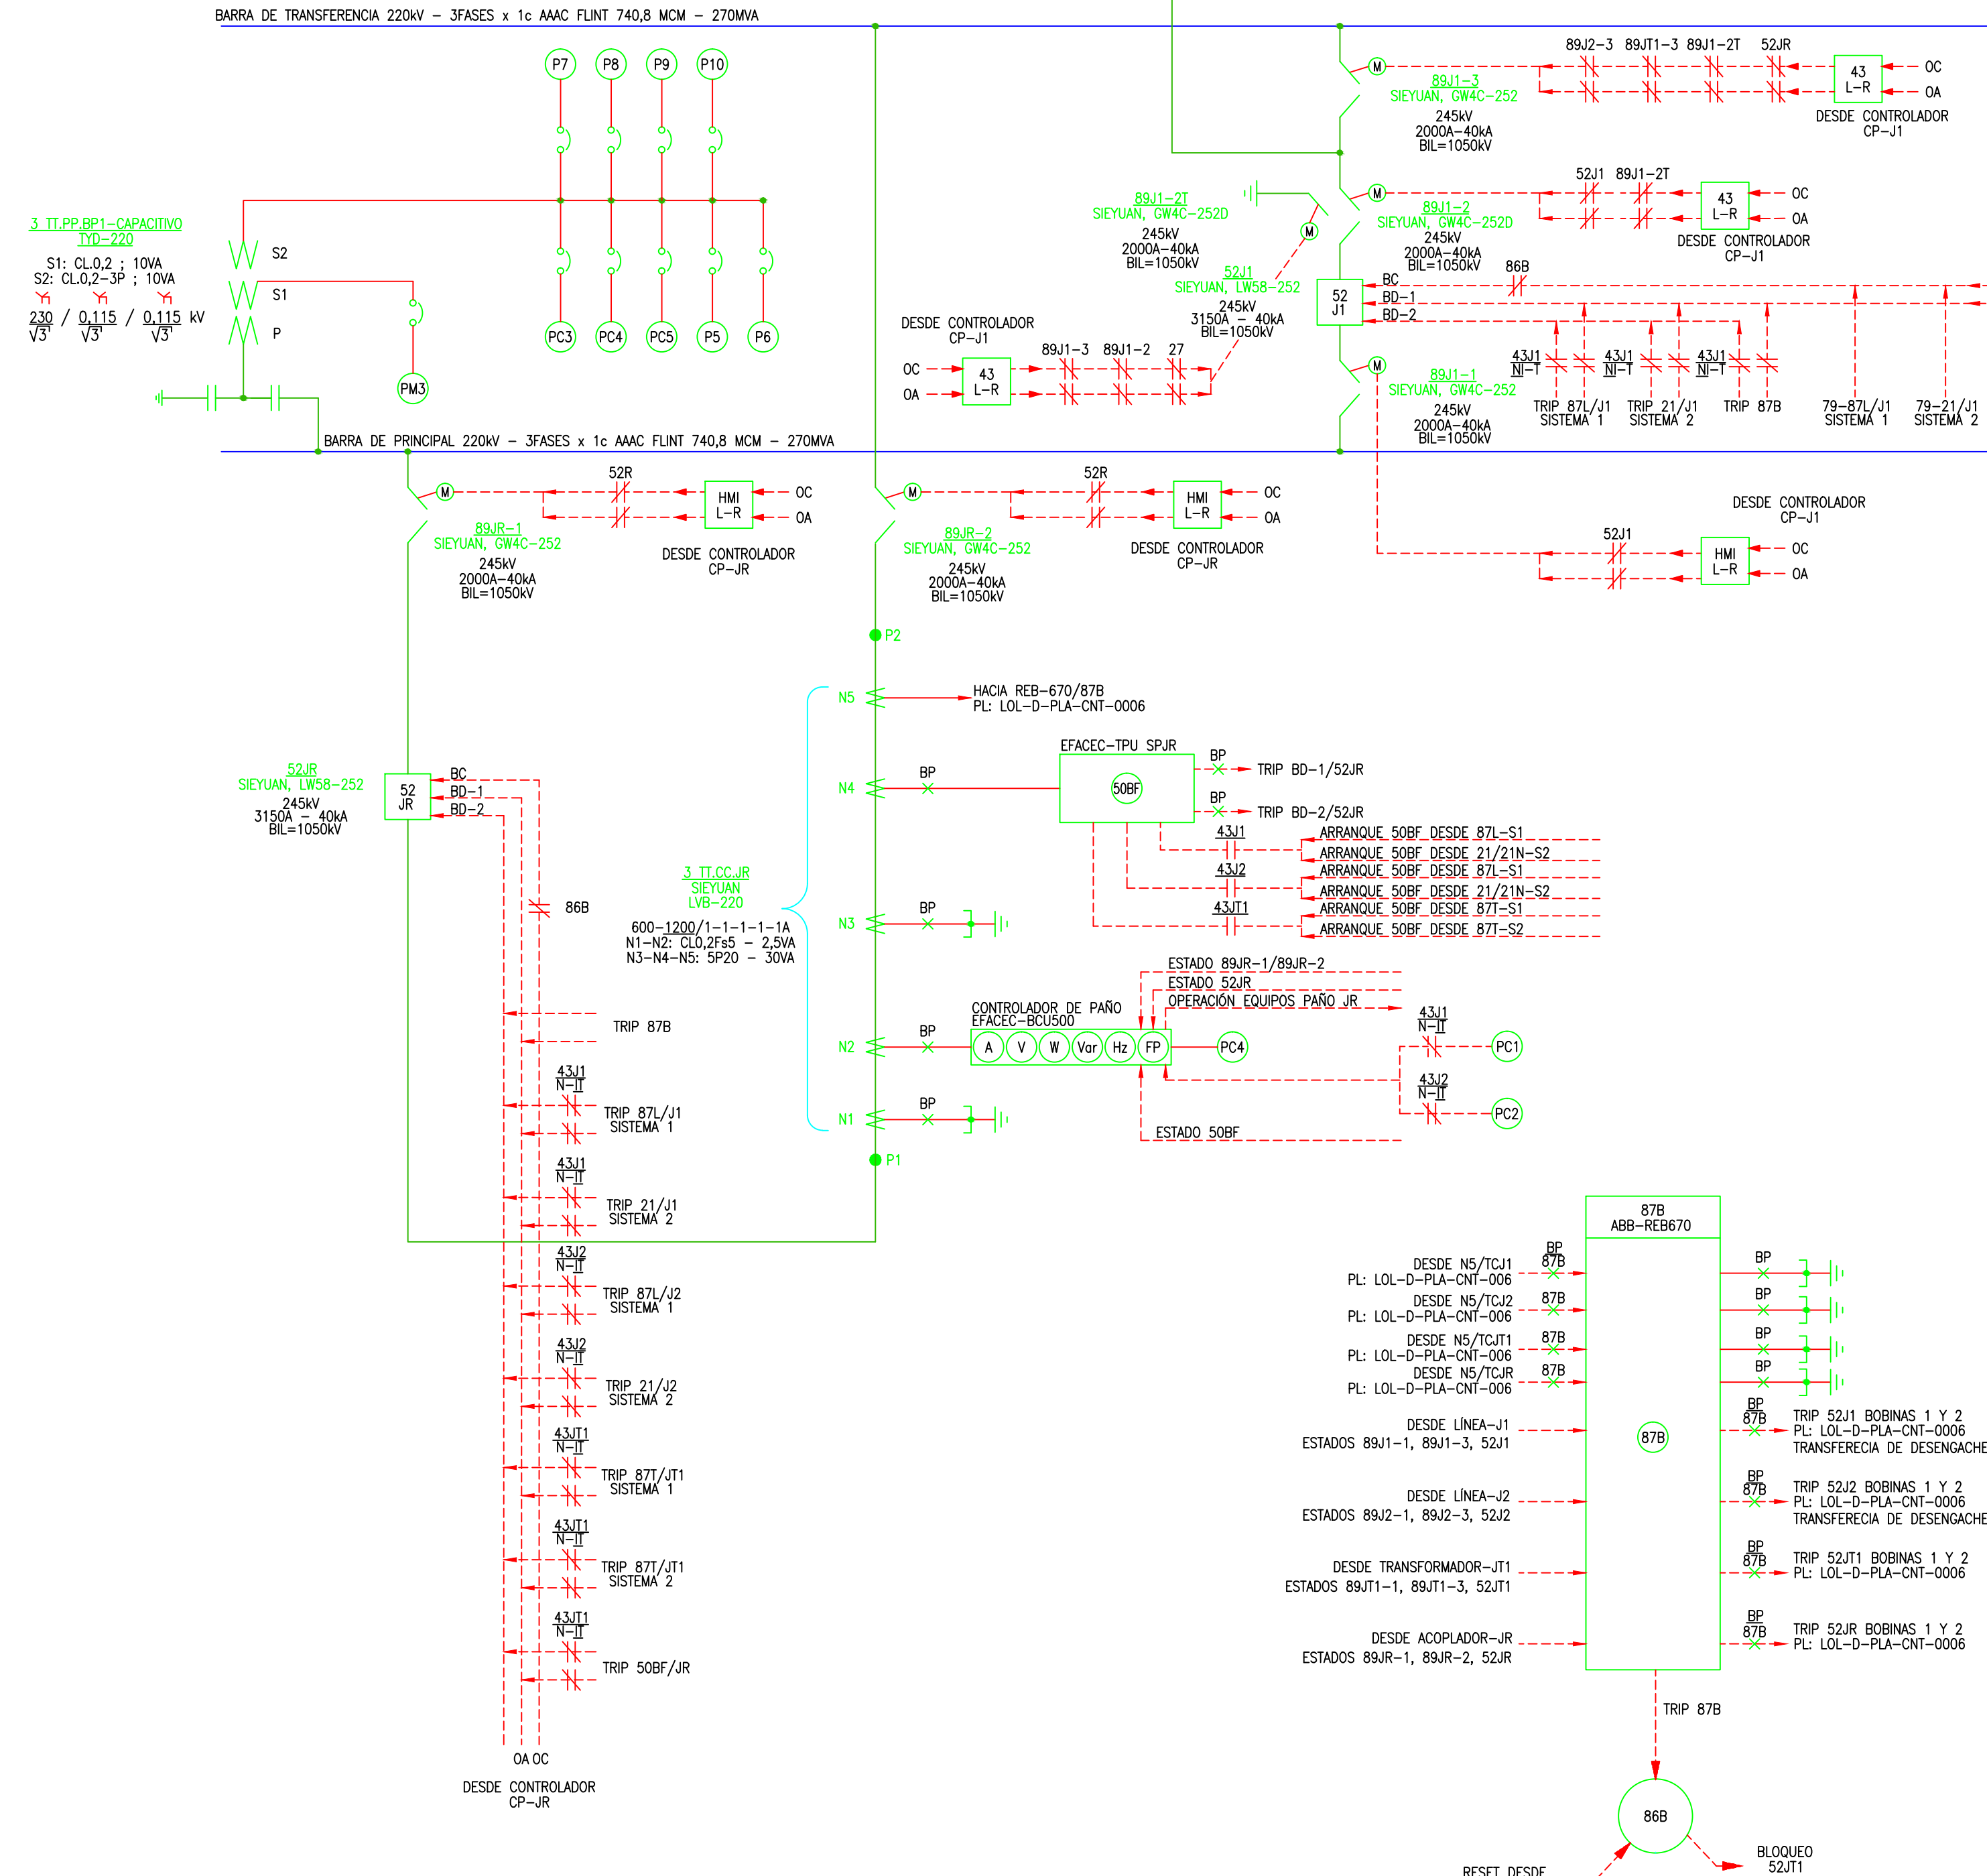


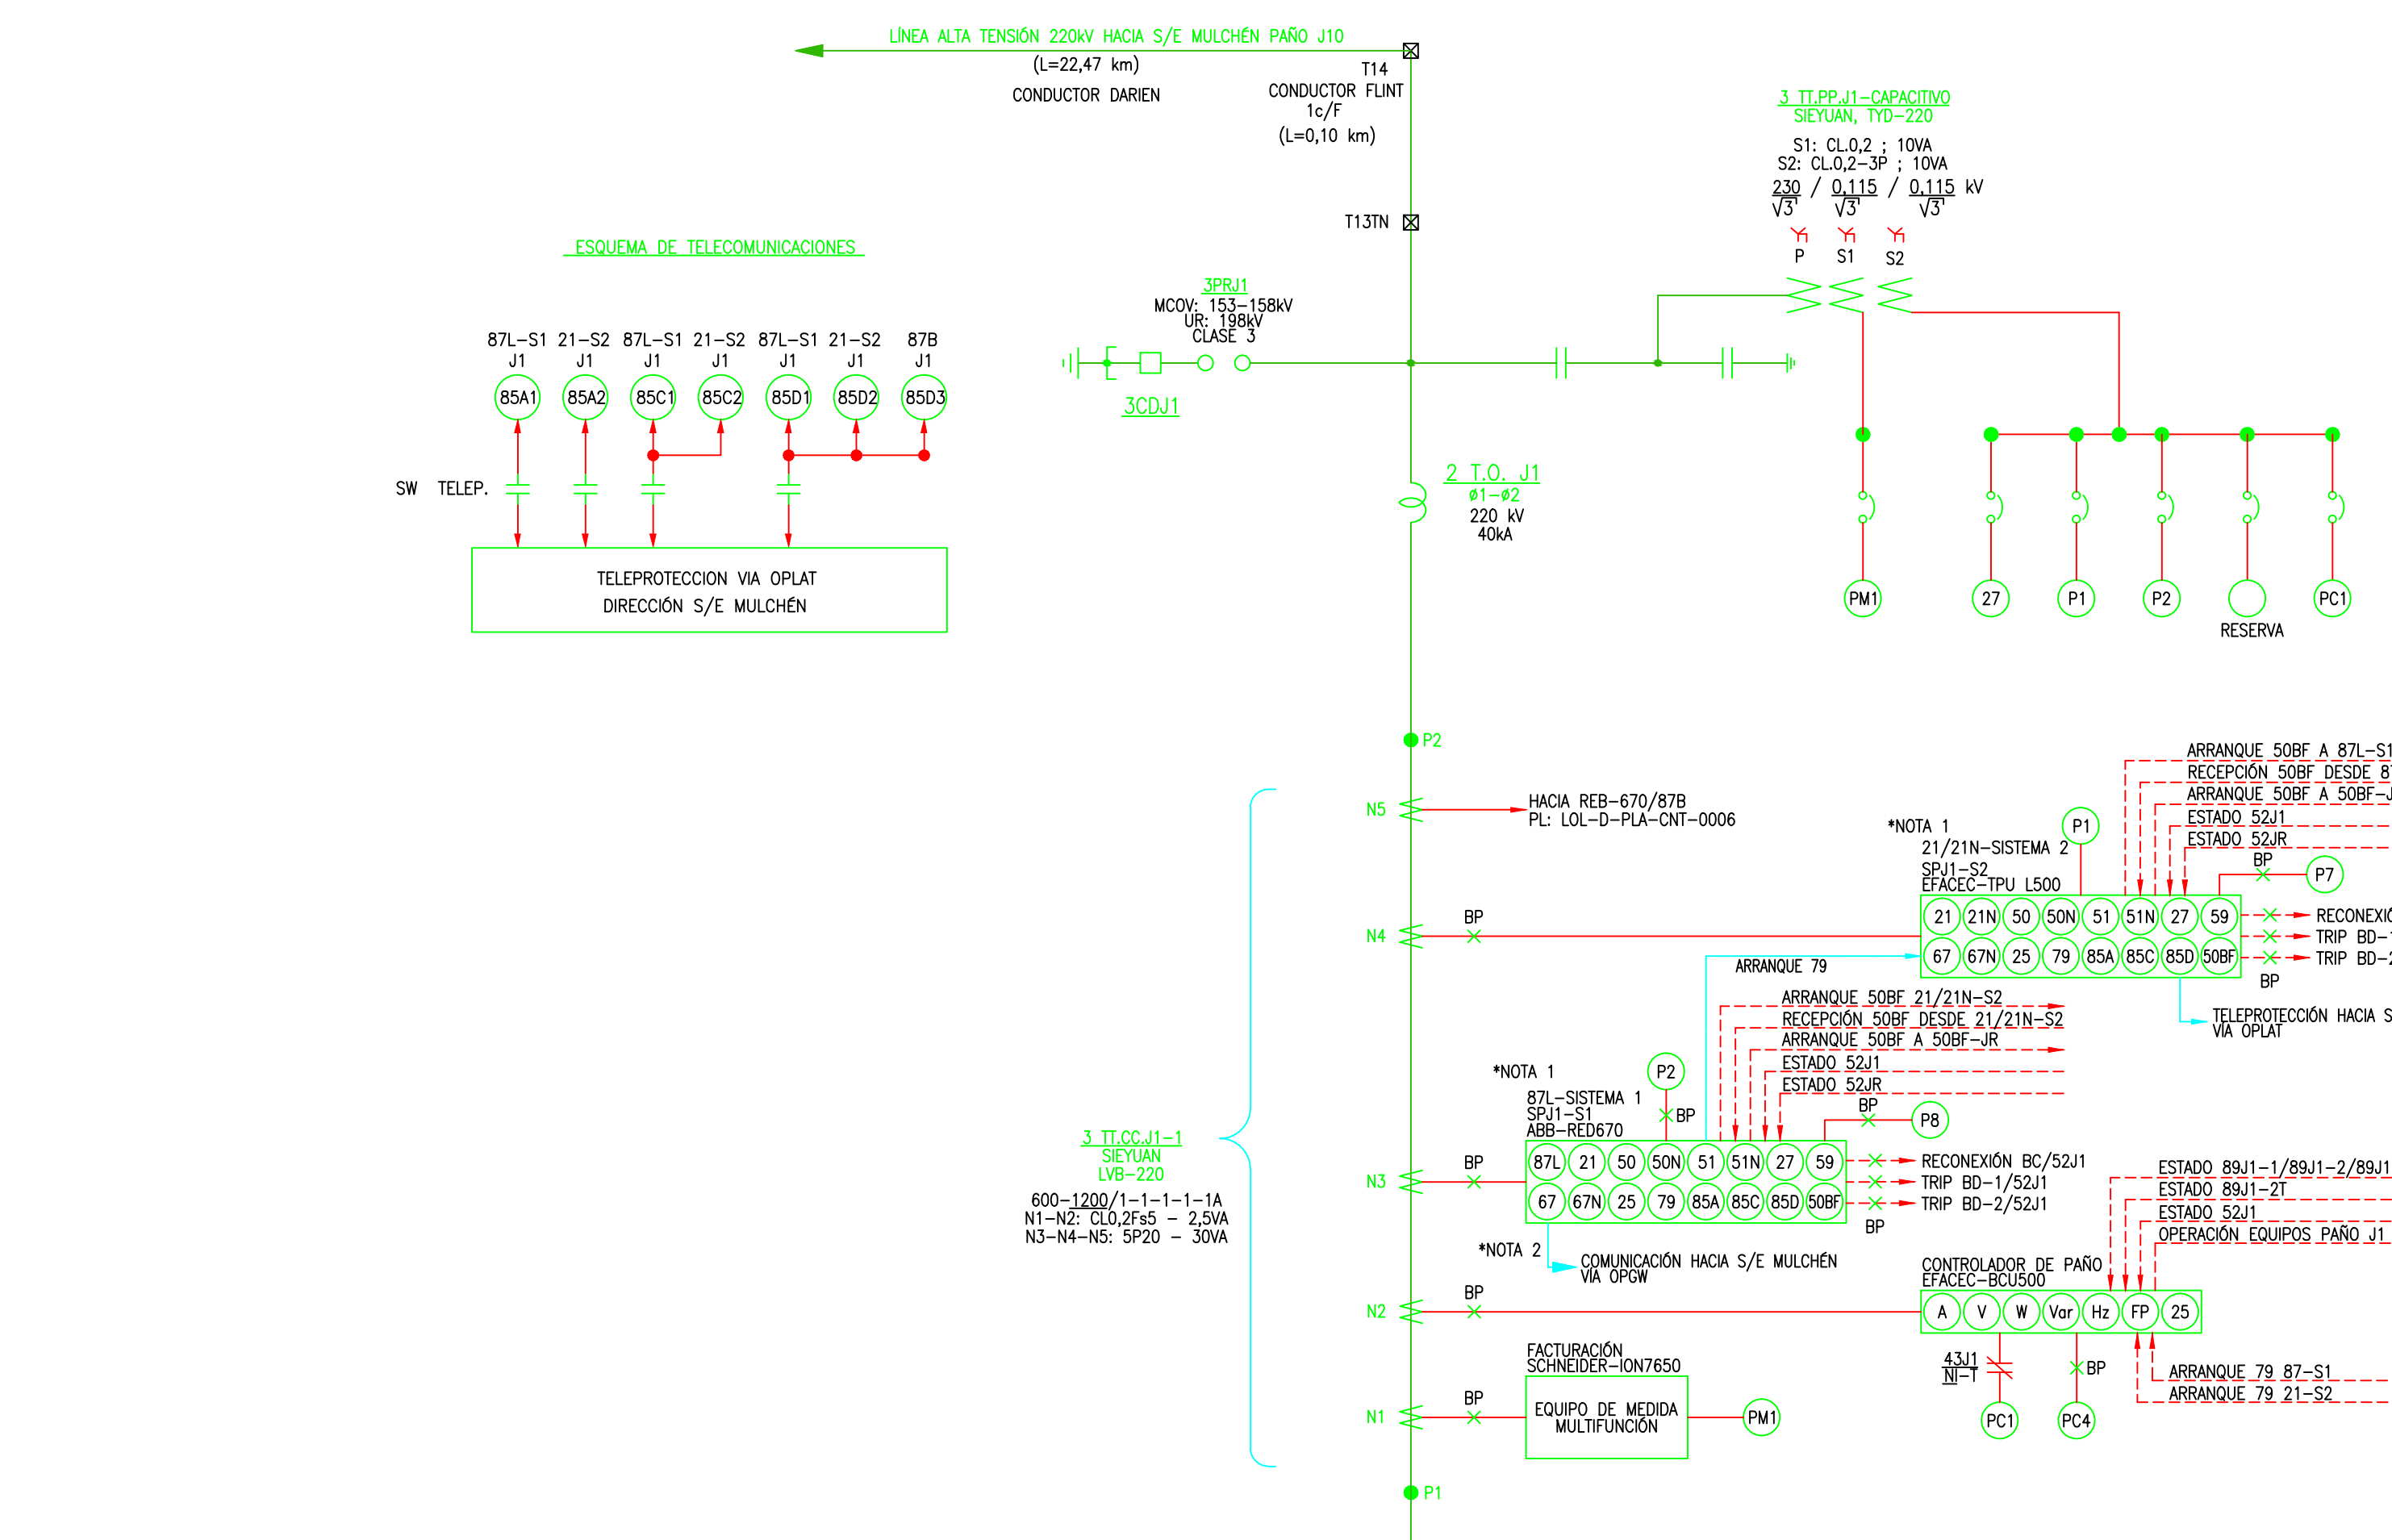

LA

INTERRUPTOR DE PODER 220 kV.

TRANSFORMADOR CON CONTADOR DE DESCARGA.

CONECTOR HORIZONTAL MOTORIZADO CON PUESTA A TIERRA.

CONECTOR HORIZONTAL MOTORIZADO.

TRANSFORMADOR DE CORRIENTE TOROIDAL.

TRANSFORMADOR DE POTENCIAL.

TRANSFORMADOR DE CORRIENTE.

PUESTA A TIERRA.

TRANSFORMADOR XLPE 34,5kV

TRANSFORMADOR SF6 / XLPE 34,5kV

TRANSFORMADOR DE ACOPLAMIENTO

FILTRO DE ONDA

TRANSFORMADOR

PRUEBA

NOMENCLATURA

MOTORIZADO

ECCIÓN DE DISTANCIA

ECCIÓN DIRECCIONAL

INDICADOR DE SINCRONISMO

ECCIÓN BAJA VOLTAJE

ECCIÓN SOBRE VOLTAJE

ECCIÓN FALLA APERTURA DE INTERRUPTOR

ECCIÓN SOBRECORRIENTE TEMPORIZADA

ECCIÓN SOBRECORRIENTE INSTANTANEA

UNIÓN

ECCIÓN DIFERENCIAL

ECCIÓN DE FRECUENCIA

TEMPERATURAS DEL TRANSFORMADOR

BUCHOLZ DEL TRANSFORMADOR

DE ACEITE DEL TRANSFORMADOR

CARGA SOBRE PRESIÓN DEL TRANSFORMADOR

TEMPERATURA DEL ACEITE

REGULACIÓN DE ZONA

DIRECCIONAL

REFERENCIA DE DESENGANCHE DIRECTO (TDO)

MAESTRO

PRUEBA

CONTROLADOR DE PAÍO

EN TÉRMICA

REGULADOR DE TENSIÓN

Gener

energía inteligente

INSTALACIÓN:

SUBSTACIÓN LOS OLMO

LOS OLMO

20/33 kV

DESCRIPCIÓN:

DIAGRAMA UNILINEAL FUNCIONAL  
SUBSTACIÓN LOS OLMO 220/33KV  
PATIO 220KV

L0L-D-PLA-CNT-0006

FECHA:

FECHA: