


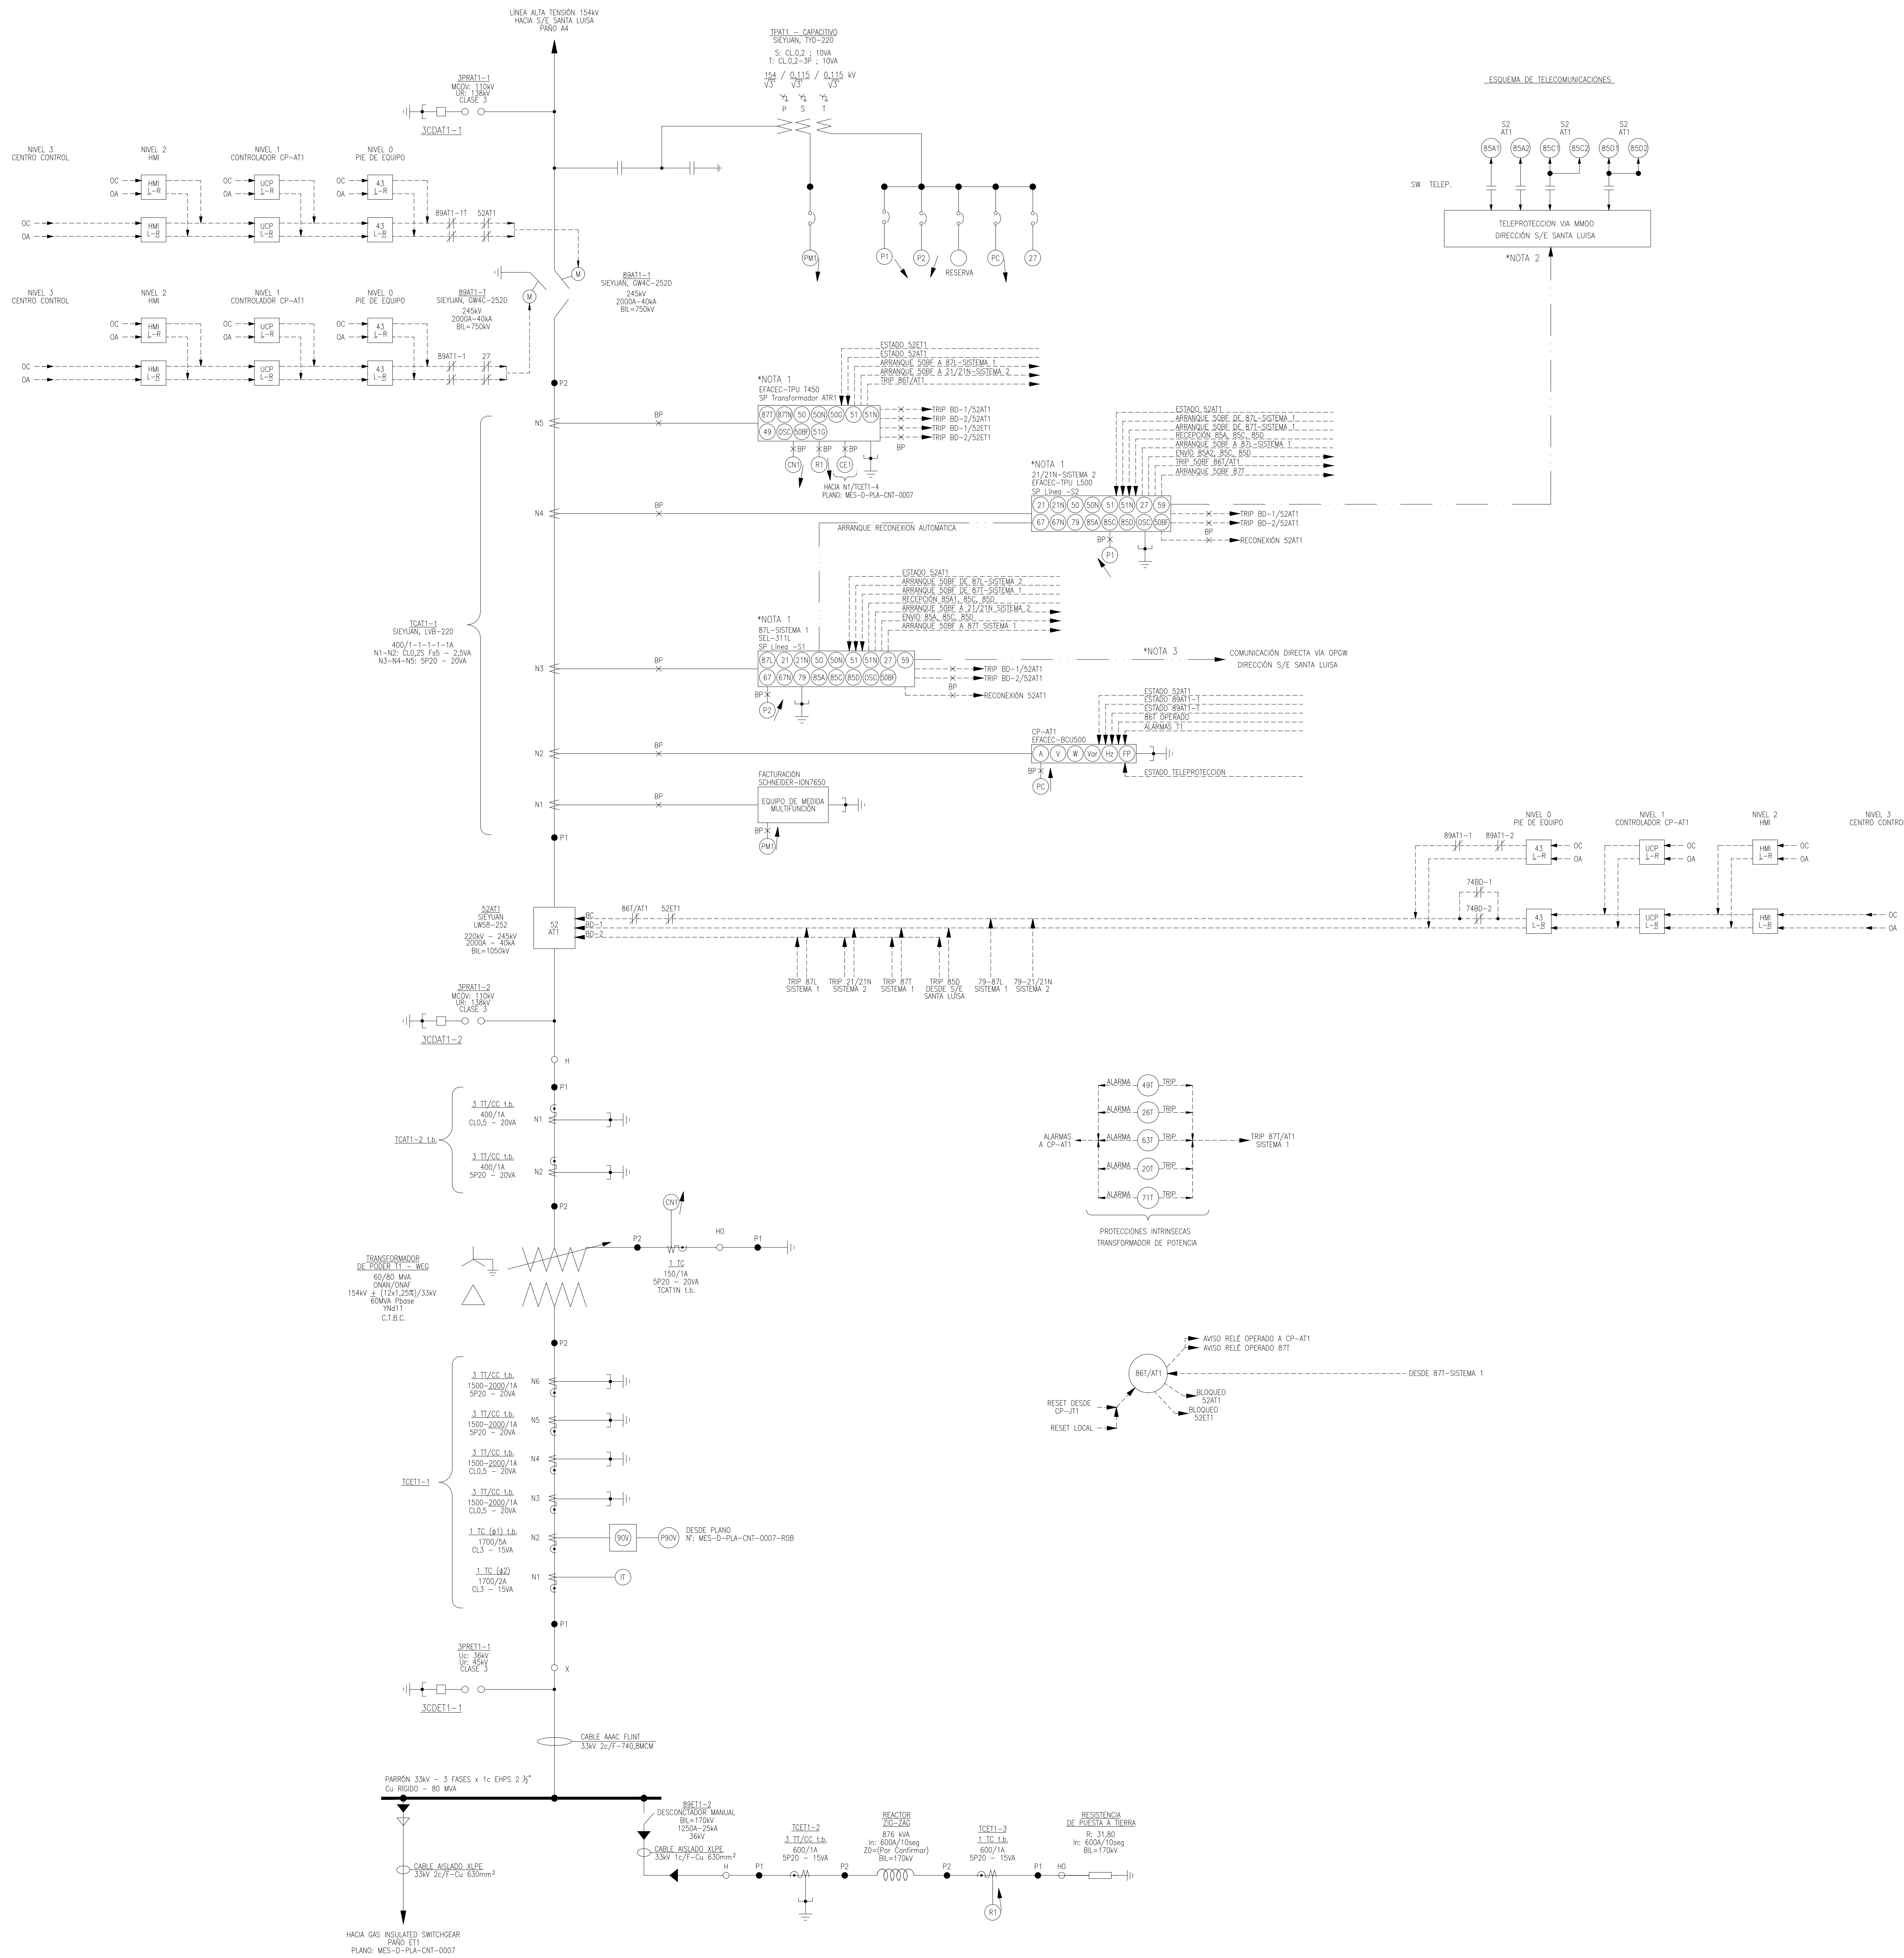

SIMBOLOGÍA

- 52 : INTERRUPTOR DE PODER 220 KV.
- □ ▢ ▣ : PARARRAYO CON CONTADOR DE DESCARGA.
- ⊖ : DESCONECTOR HORIZONTAL MOTORIZADO CON PUESTA A TIERRA.
- ⊕ : DESCONECTOR HORIZONTAL MOTORIZADO.
- ⊗ : TRANSFORMADOR DE CORRIENTE TOROIDAL.
- ⊞ : TRANSFORMADOR DE POTENCIAL.
- ⊞ : TRANSFORMADOR DE CORRIENTE.
- ⊞ : RESISTENCIA PUESTA A TIERRA.
- △ : CONECTOR XLPE 34,5kV
- ▲ : CONECTOR SF6 / XLPE 34,5kV

NOMENCLATURA

- Ⓜ MECANISMO MOTORIZADO
- 21/21N PROTECCIÓN DE DISTANCIA
- 67 PROTECCIÓN DIRECCIONAL
- 25 VERIFICADOR DE SINCRONISMO
- 27 PROTECCIÓN BAJO VOLTAJE
- 59 PROTECCIÓN SOBRE VOLTAJE
- 50B8 PROTECCIÓN FALLA APERTURA DE INTERRUPTOR
- 51 PROTECCIÓN SOBRECORRIENTE TEMPORIZADA
- 50 PROTECCIÓN SOBRECORRIENTE INSTANTANEA
- 79 RECONEXIÓN
- 87 PROTECCIÓN DIFERENCIAL
- 81 PROTECCIÓN DE FRECUENCIA
- 49T TEMPERATURA DEVANADOS DEL TRANSFORMADOR
- 63T RELÉ BUCHHOLZ DEL TRANSFORMADOR
- 71T NIVEL DE ACEITE DEL TRANSFORMADOR
- 20T DESCARGA SOBRE PRESIÓN DEL TRANSFORMADOR
- 26T TEMPERATURA DEL ACEITE
- 85A ACCELERACIÓN DE ZONA
- 85C COMPARACIÓN DIRECCIONAL
- 85D TRANSFERENCIA DE DESENGANCHE DIRECTO (TDO)
- 86 RELÉ MAESTRO
- BP BLOQUE DE PRUEBA
- CP CONTROLADOR DE PAÑO
- IT IMAGEN TÉRMICA
- 90V REGULADOR DE TENSION
- OSC OSCILOPURTURBOGRÁFO

- NOTAS:
- 1.- LAS FUNCIONES QUE SERÁN HABILITADAS SE CONFIRMARÁ CON ESTUDIO DE COORDINACIÓN Y AJUSTE DE PROTECCIONES.
 - 2.- COMUNICACIÓN DE RESPALDO POR VÍA OPGW, EN CASO DE FALLA DEL SISTEMA MM00, PARA DETALLES VER PLANO MES-D-PLA-CNT-0005.
 - 3.- LA PROTECCIÓN DIFERENCIAL DE LÍNEA SEL-311L ESTÁ EN CAPACIDAD DE REALIZAR TELECOMANDOS A TRAVÉS DEL ENLAJE QUE UTILIZA PARA EL ESQUEMA DIFERENCIAL DE LÍNEA.

N°	FECHA	MODIFICACIONES	EJEC	REV	APR
03	17.09.20	EMITIDO PARA CONSTRUCCIÓN	E.S.O.	A.R.H.	C.Y.O.
02	16.09.20	EMITIDO PARA CONSTRUCCIÓN (ACTUALIZADO ABENGOA)	ABENGOA	ABENGOA	ABENGOA
01	24.08.20	EMITIDO PARA CONSTRUCCIÓN	E.S.O.	A.R.H.	C.Y.O.
00	02.07.20	VALIDO PARA CONSTRUCCIÓN	E.S.O.	A.R.H.	C.Y.O.
OC	01.07.20	EMITIDO PARA APROBACIÓN	E.S.O.	A.R.H.	C.Y.O.
OB	08.06.20	EMITIDO PARA APROBACIÓN	E.S.O.	A.R.H.	C.Y.O.
OA	07.05.20	EMITIDO PARA REVISIÓN Y COMENTARIOS	E.S.O.	A.R.H.	C.Y.O.
A	24.04.20	EMITIDO PARA REVISIÓN INTERNA	E.S.O.	A.R.H.	C.Y.O.

DESSAU ABENGOA CHILE

PROYECTO:	REVISO:	APROBO:	FECHA:
03	03	03	03

AES Gener		SUBESTACIÓN MESAMÁVIDA	
AREA:	S/E MESAMÁVIDA 154kV	DESCRIPCION:	DIAGRAMA UNILINEAL FUNCIONAL SUBESTACIÓN MESAMÁVIDA 154/33kV PATIO 154kV
PLANO N°	MES-D-PLA-CNT-0006		
PROYECTO:	REVISO:	APROBO:	FECHA INICIAL: 24-04-20